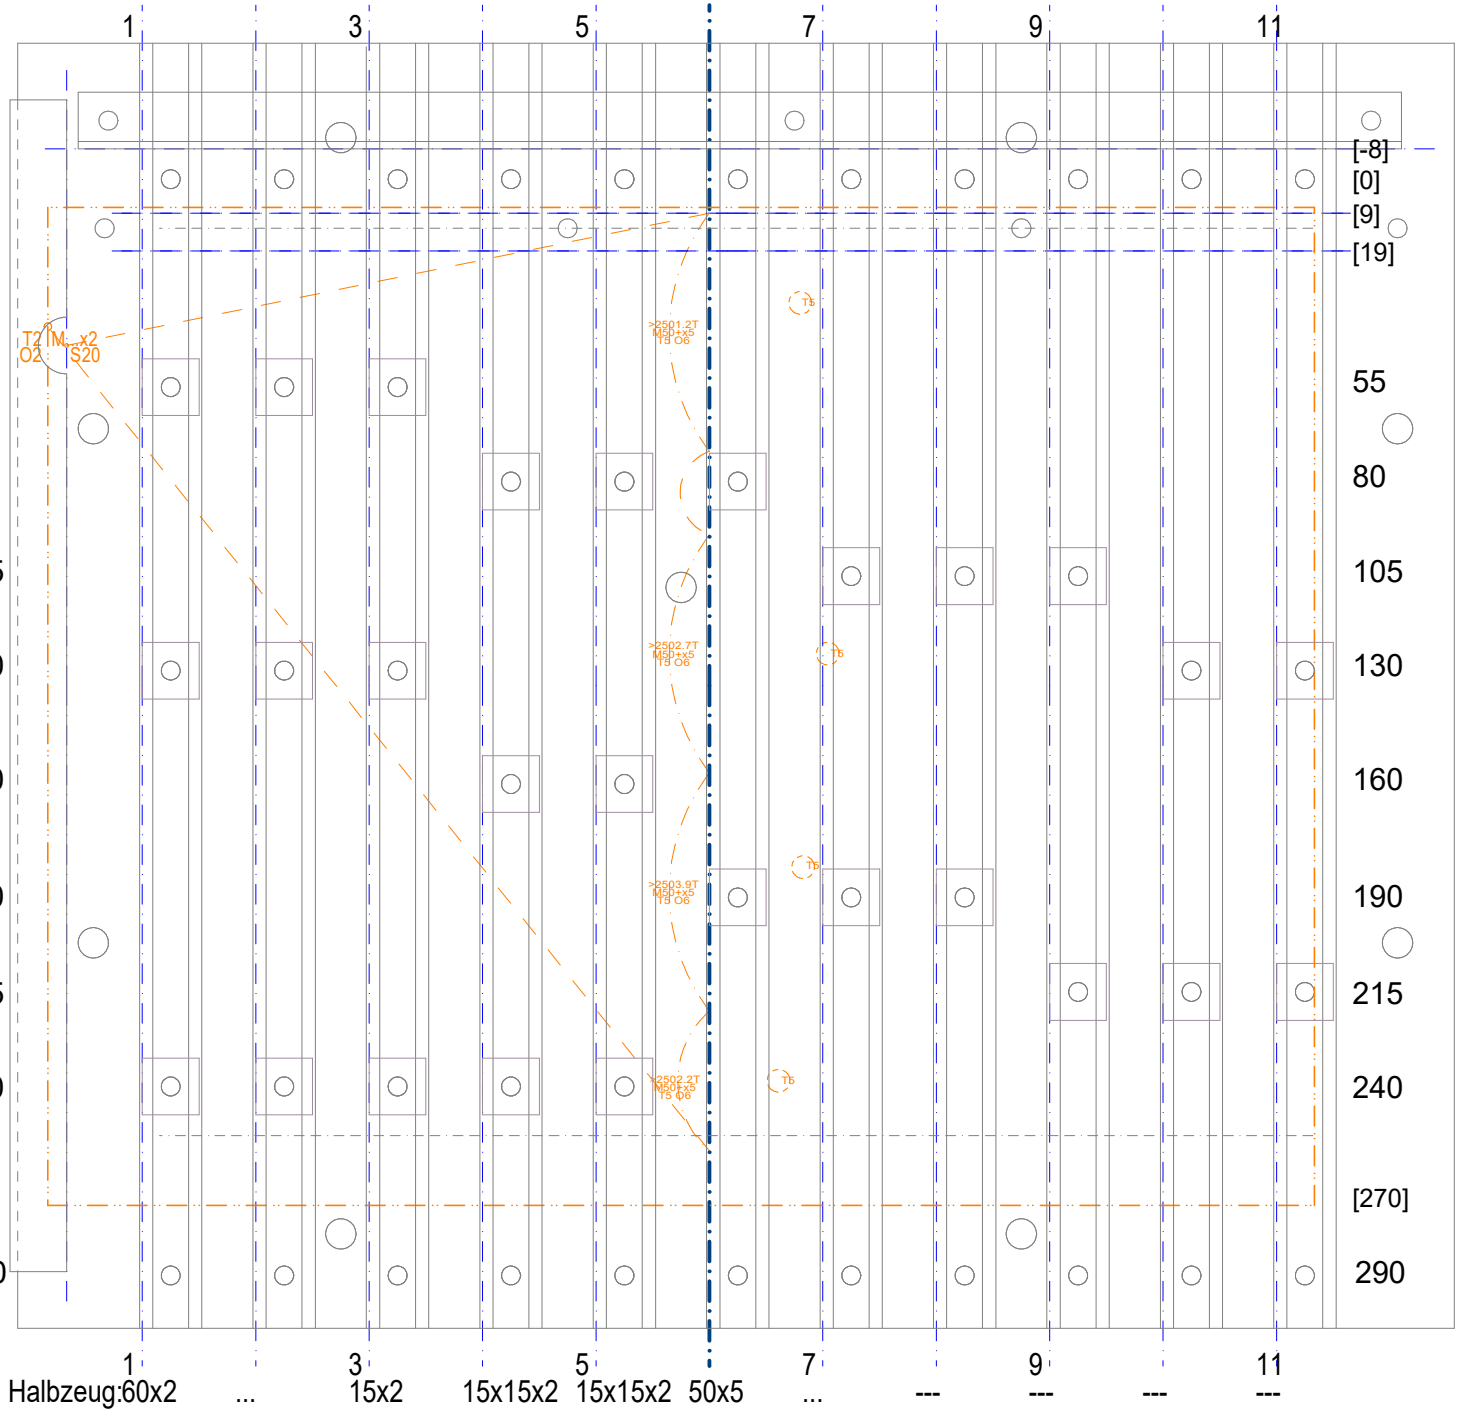


Stückliste 3808.7:

3x2501.1
1x2501.2/5
1x2501.3
1x2501.4/4
1x2501.5/S

1x2502.1
1x2502.2/5
1x2502.7/5

1x2503.1/5
1x2503.2
1x2503.3/6

Stellwerk HMM	*Maßstab 1:2*
2026-05-08	*Bl. 3808 S.7bTh*
Abtriebe Aufspannpfad	
Dateiname	3808 S.7bTh Abtriebe