


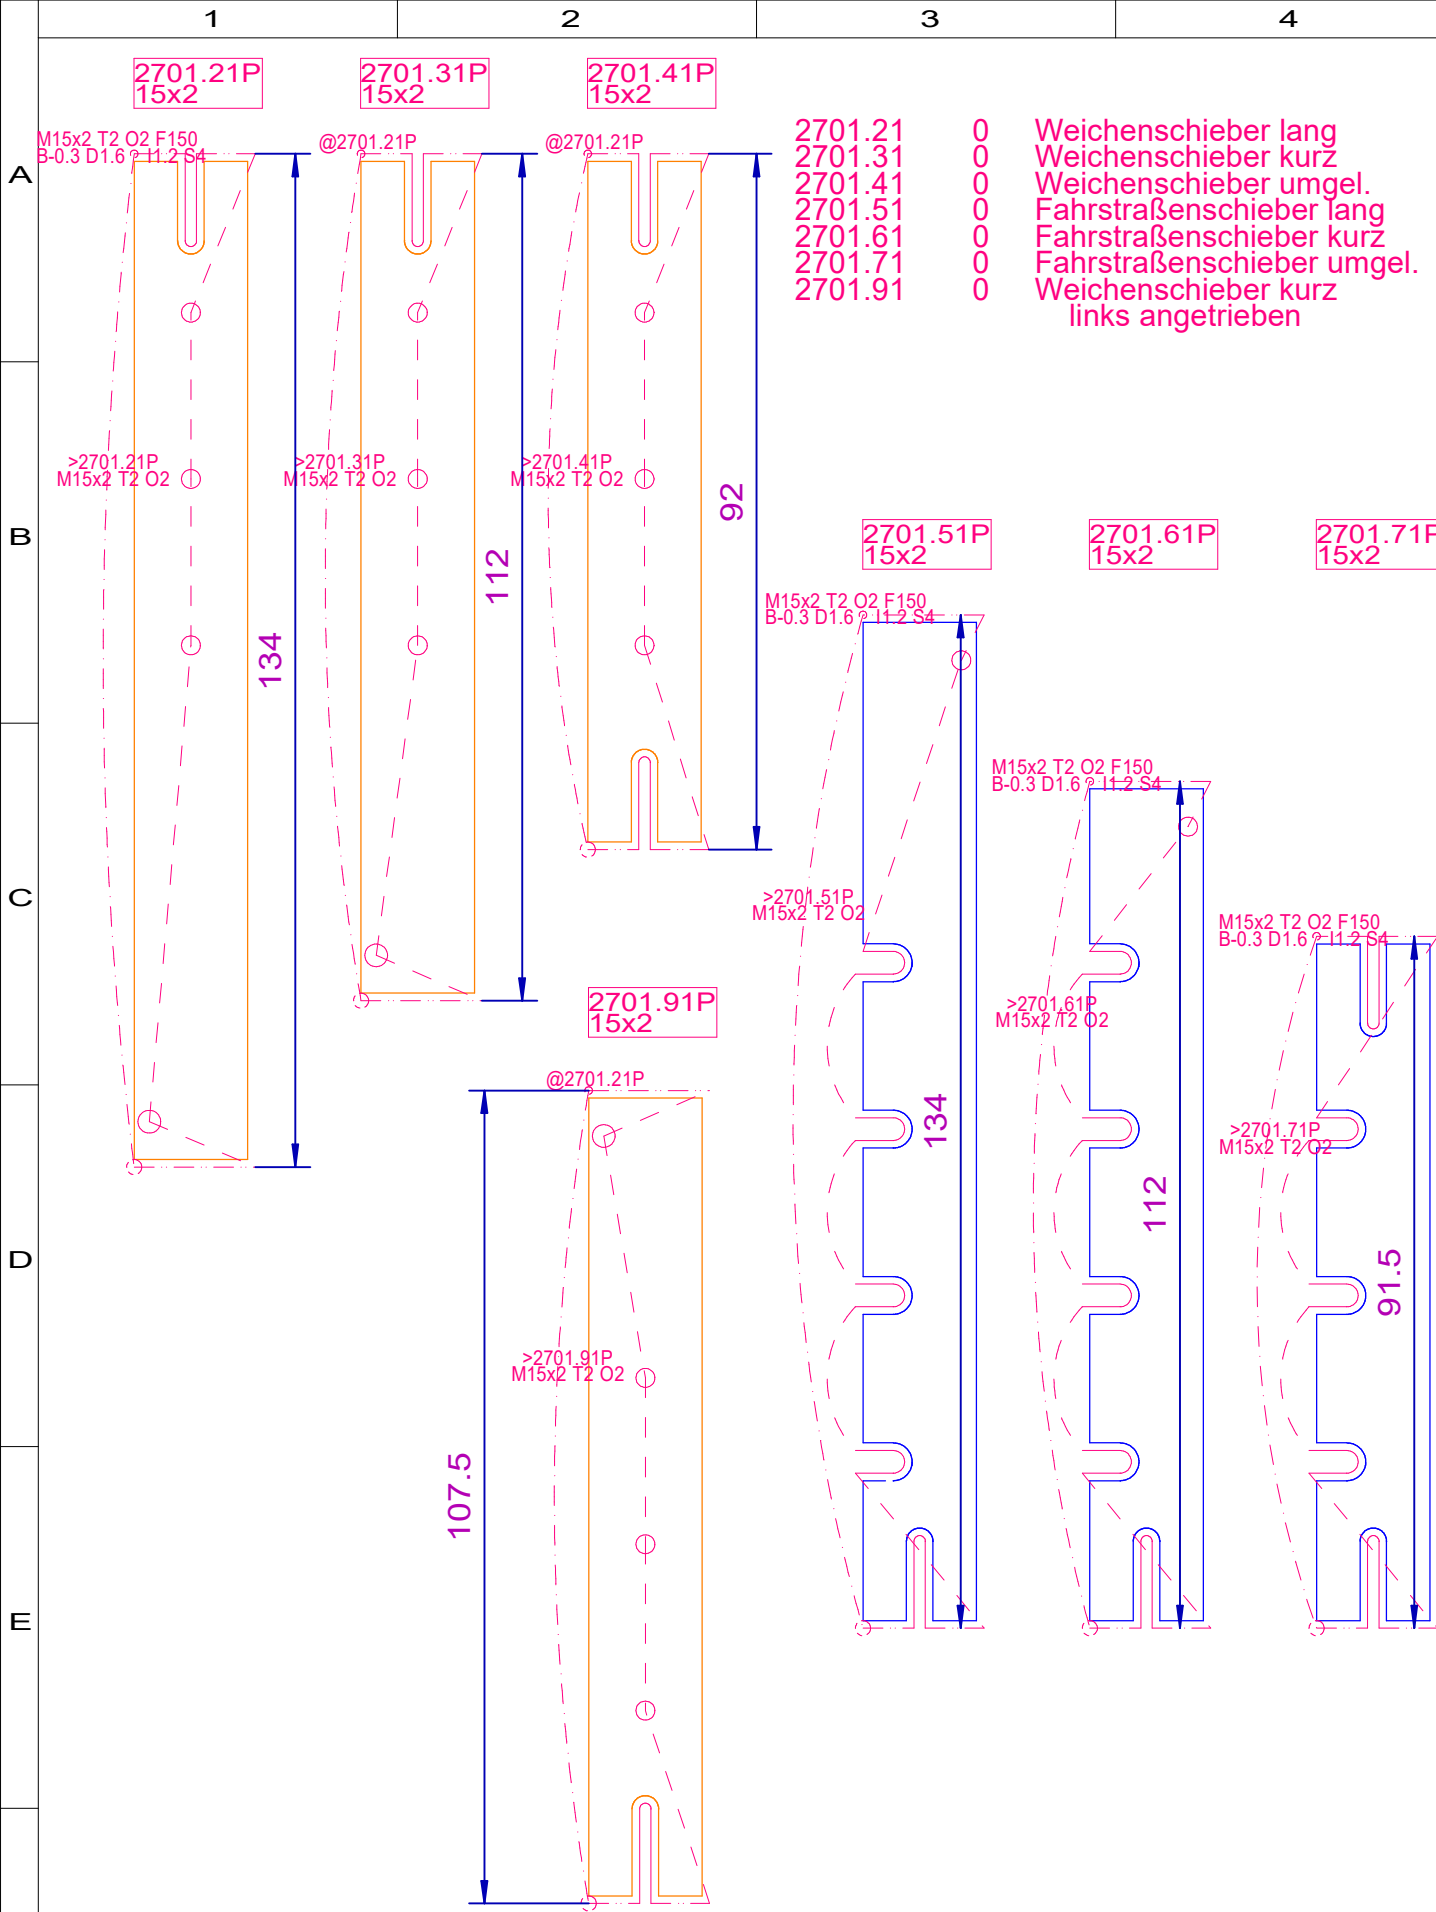

2701.21	0	Weichenschieber lang
2701.31	0	Weichenschieber kurz
2701.41	0	Weichenschieber umgel.
2701.51	0	Fahrstraßenschieber lang
2701.61	0	Fahrstraßenschieber kurz
2701.71	0	Fahrstraßenschieber umgel.
2701.91	0	Weichenschieber kurz links angetrieben

Stellwerk HMM	2026-09-24	Maßstab 1:1
Bl. 2701 P.3v	Zentralschloss Schieber Länge 1	
Dateiname	2701 P.3v Zentralschlossschieber Länge 1	