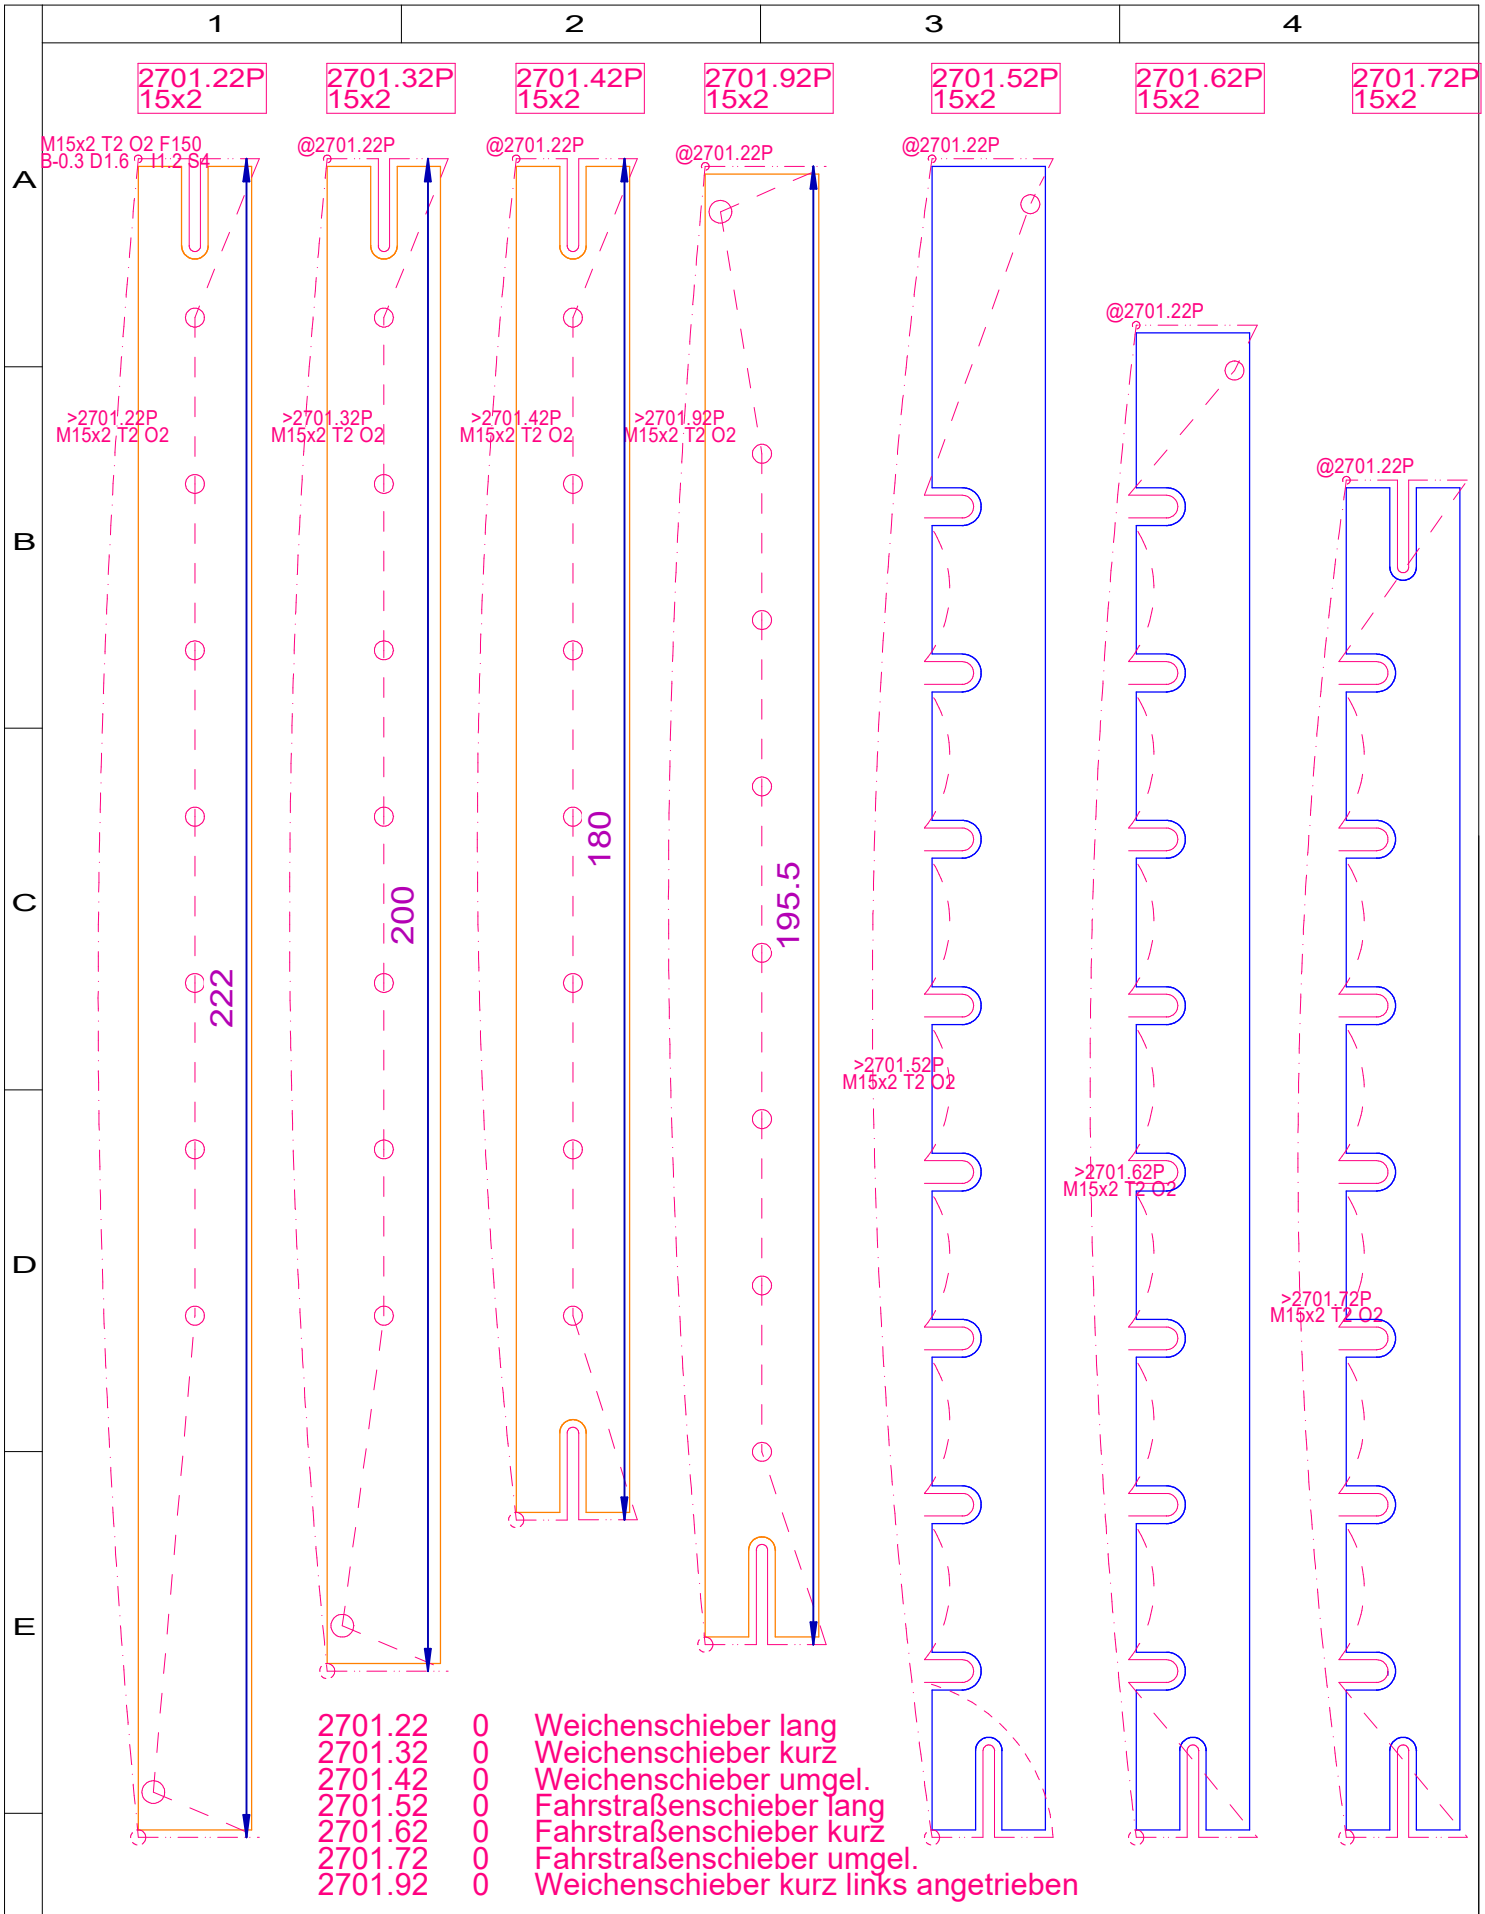


2701.22	0	Weichenschieber lang
2701.32	0	Weichenschieber kurz
2701.42	0	Weichenschieber umgel.
2701.52	0	Fahrstraßenschieber lang
2701.62	0	Fahrstraßenschieber kurz
2701.72	0	Fahrstraßenschieber umgel.
2701.92	0	Weichenschieber kurz links angetrieben

Stellwerk HMM	2026-09-24	*Maßstab 1:1*
Bl. 2701 P.4v	*Zentralschloss Schieber Länge 2*	
Dateiname	2701 P.4v Zentralschlossschieber Länge 2	