


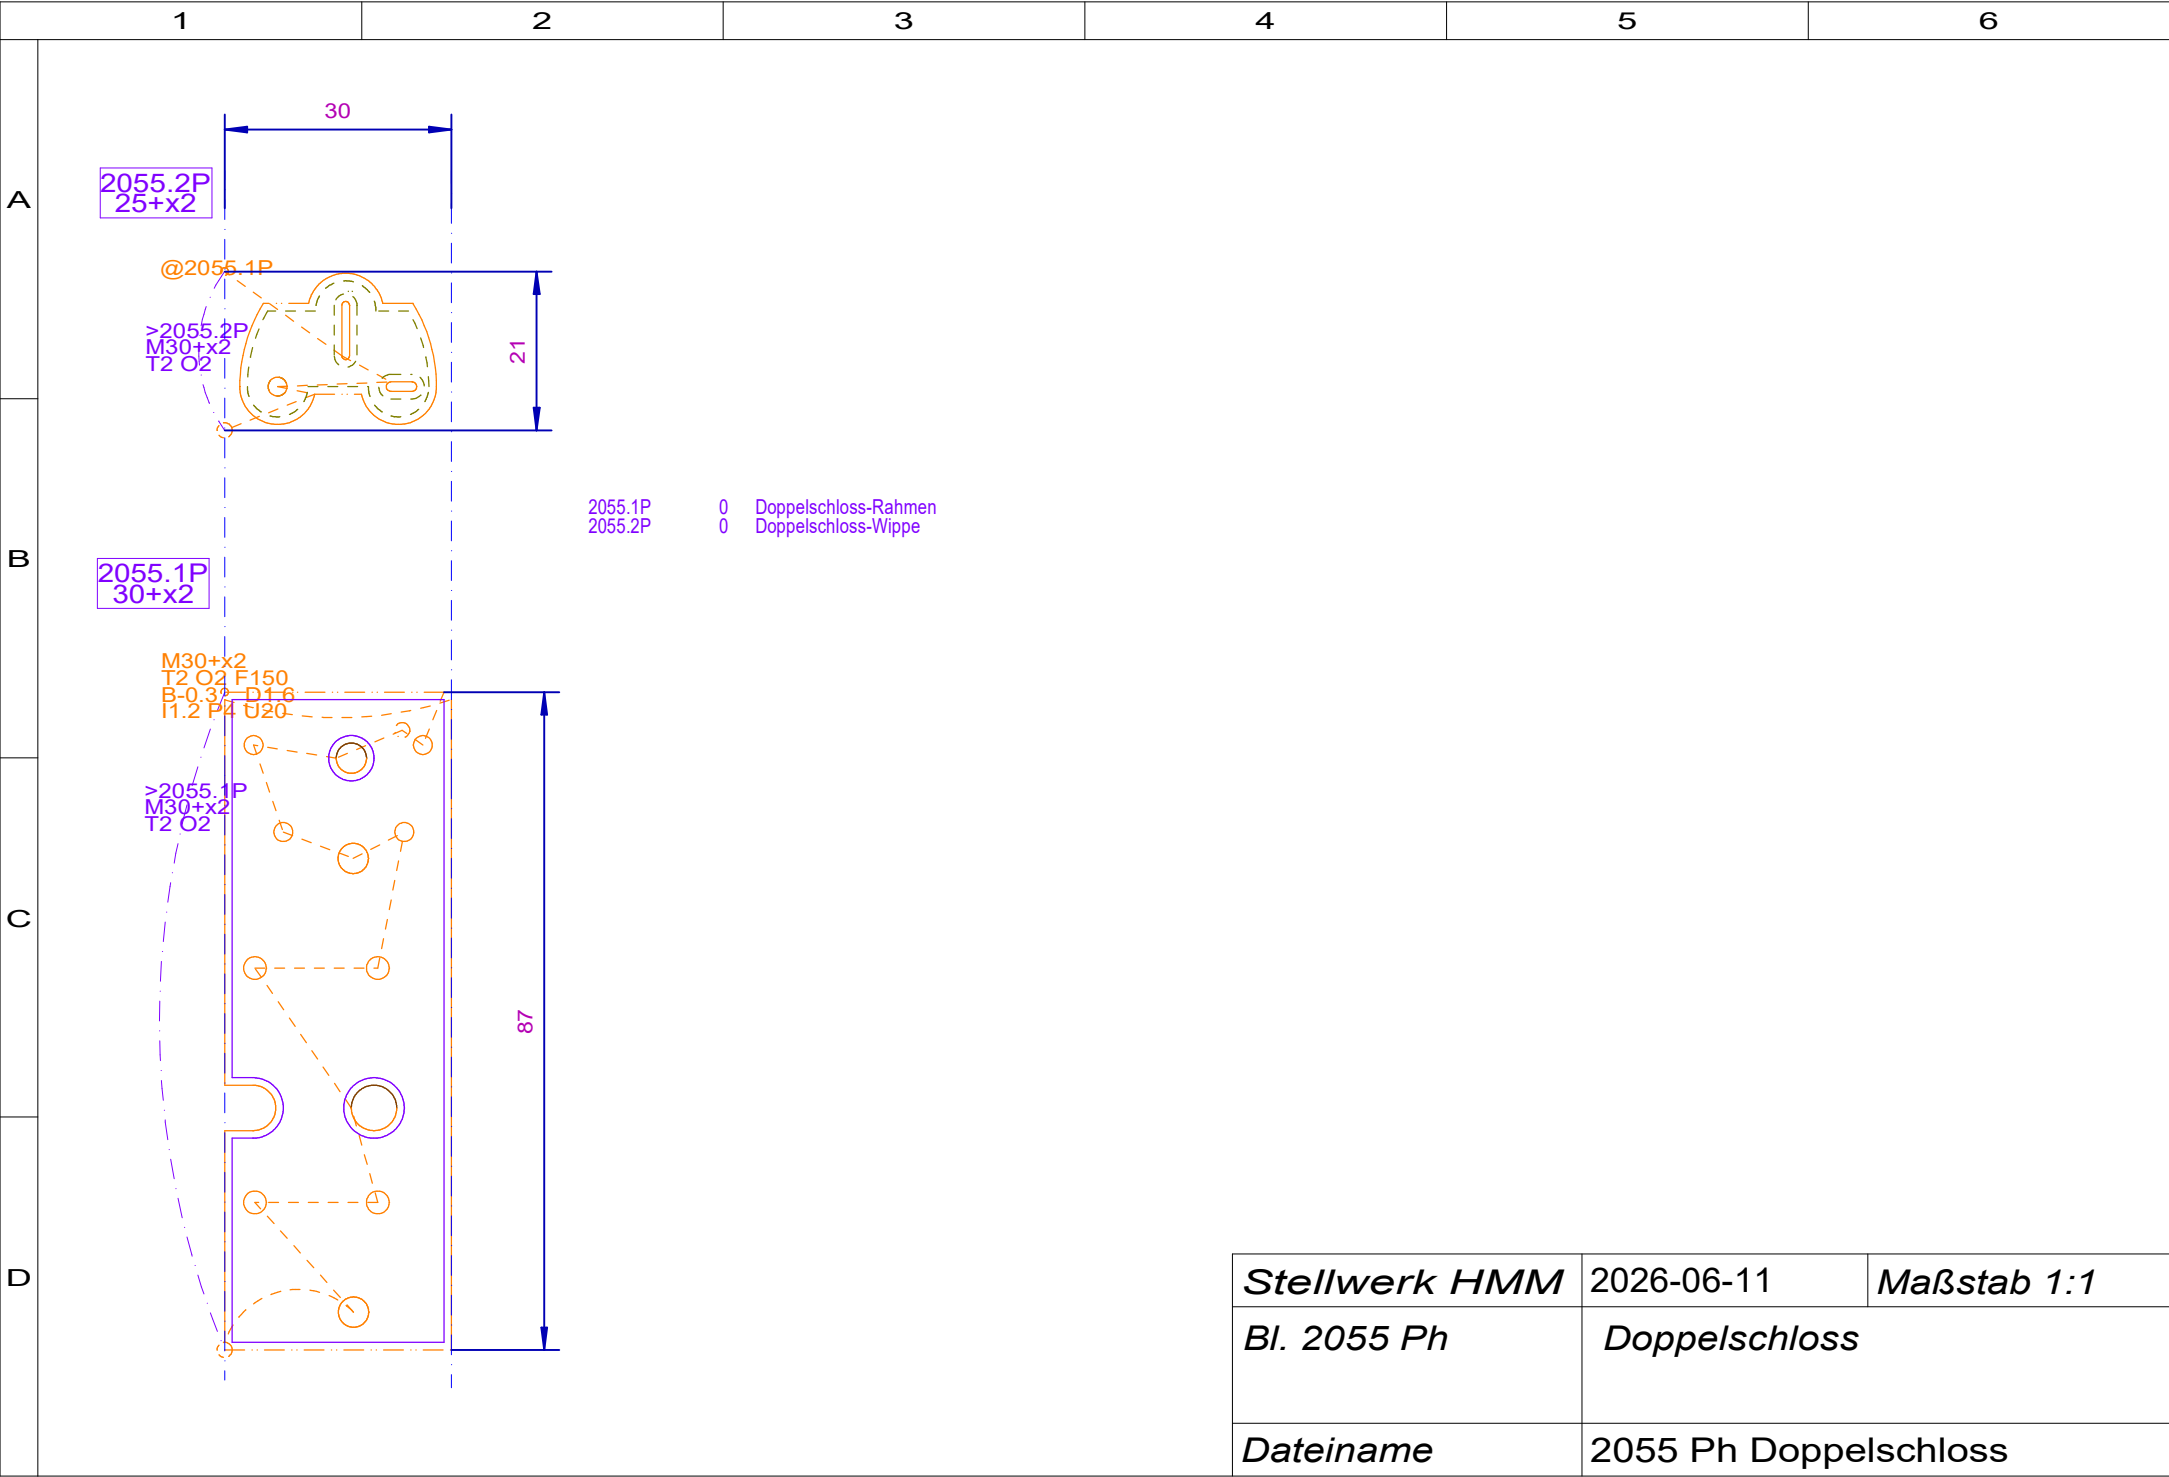

Stellwerk HMM	2026-06-11	Maßstab 1:1
Bl. 2055 Ph	Doppelschloss	
Dateiname	2055 Ph Doppelschloss	