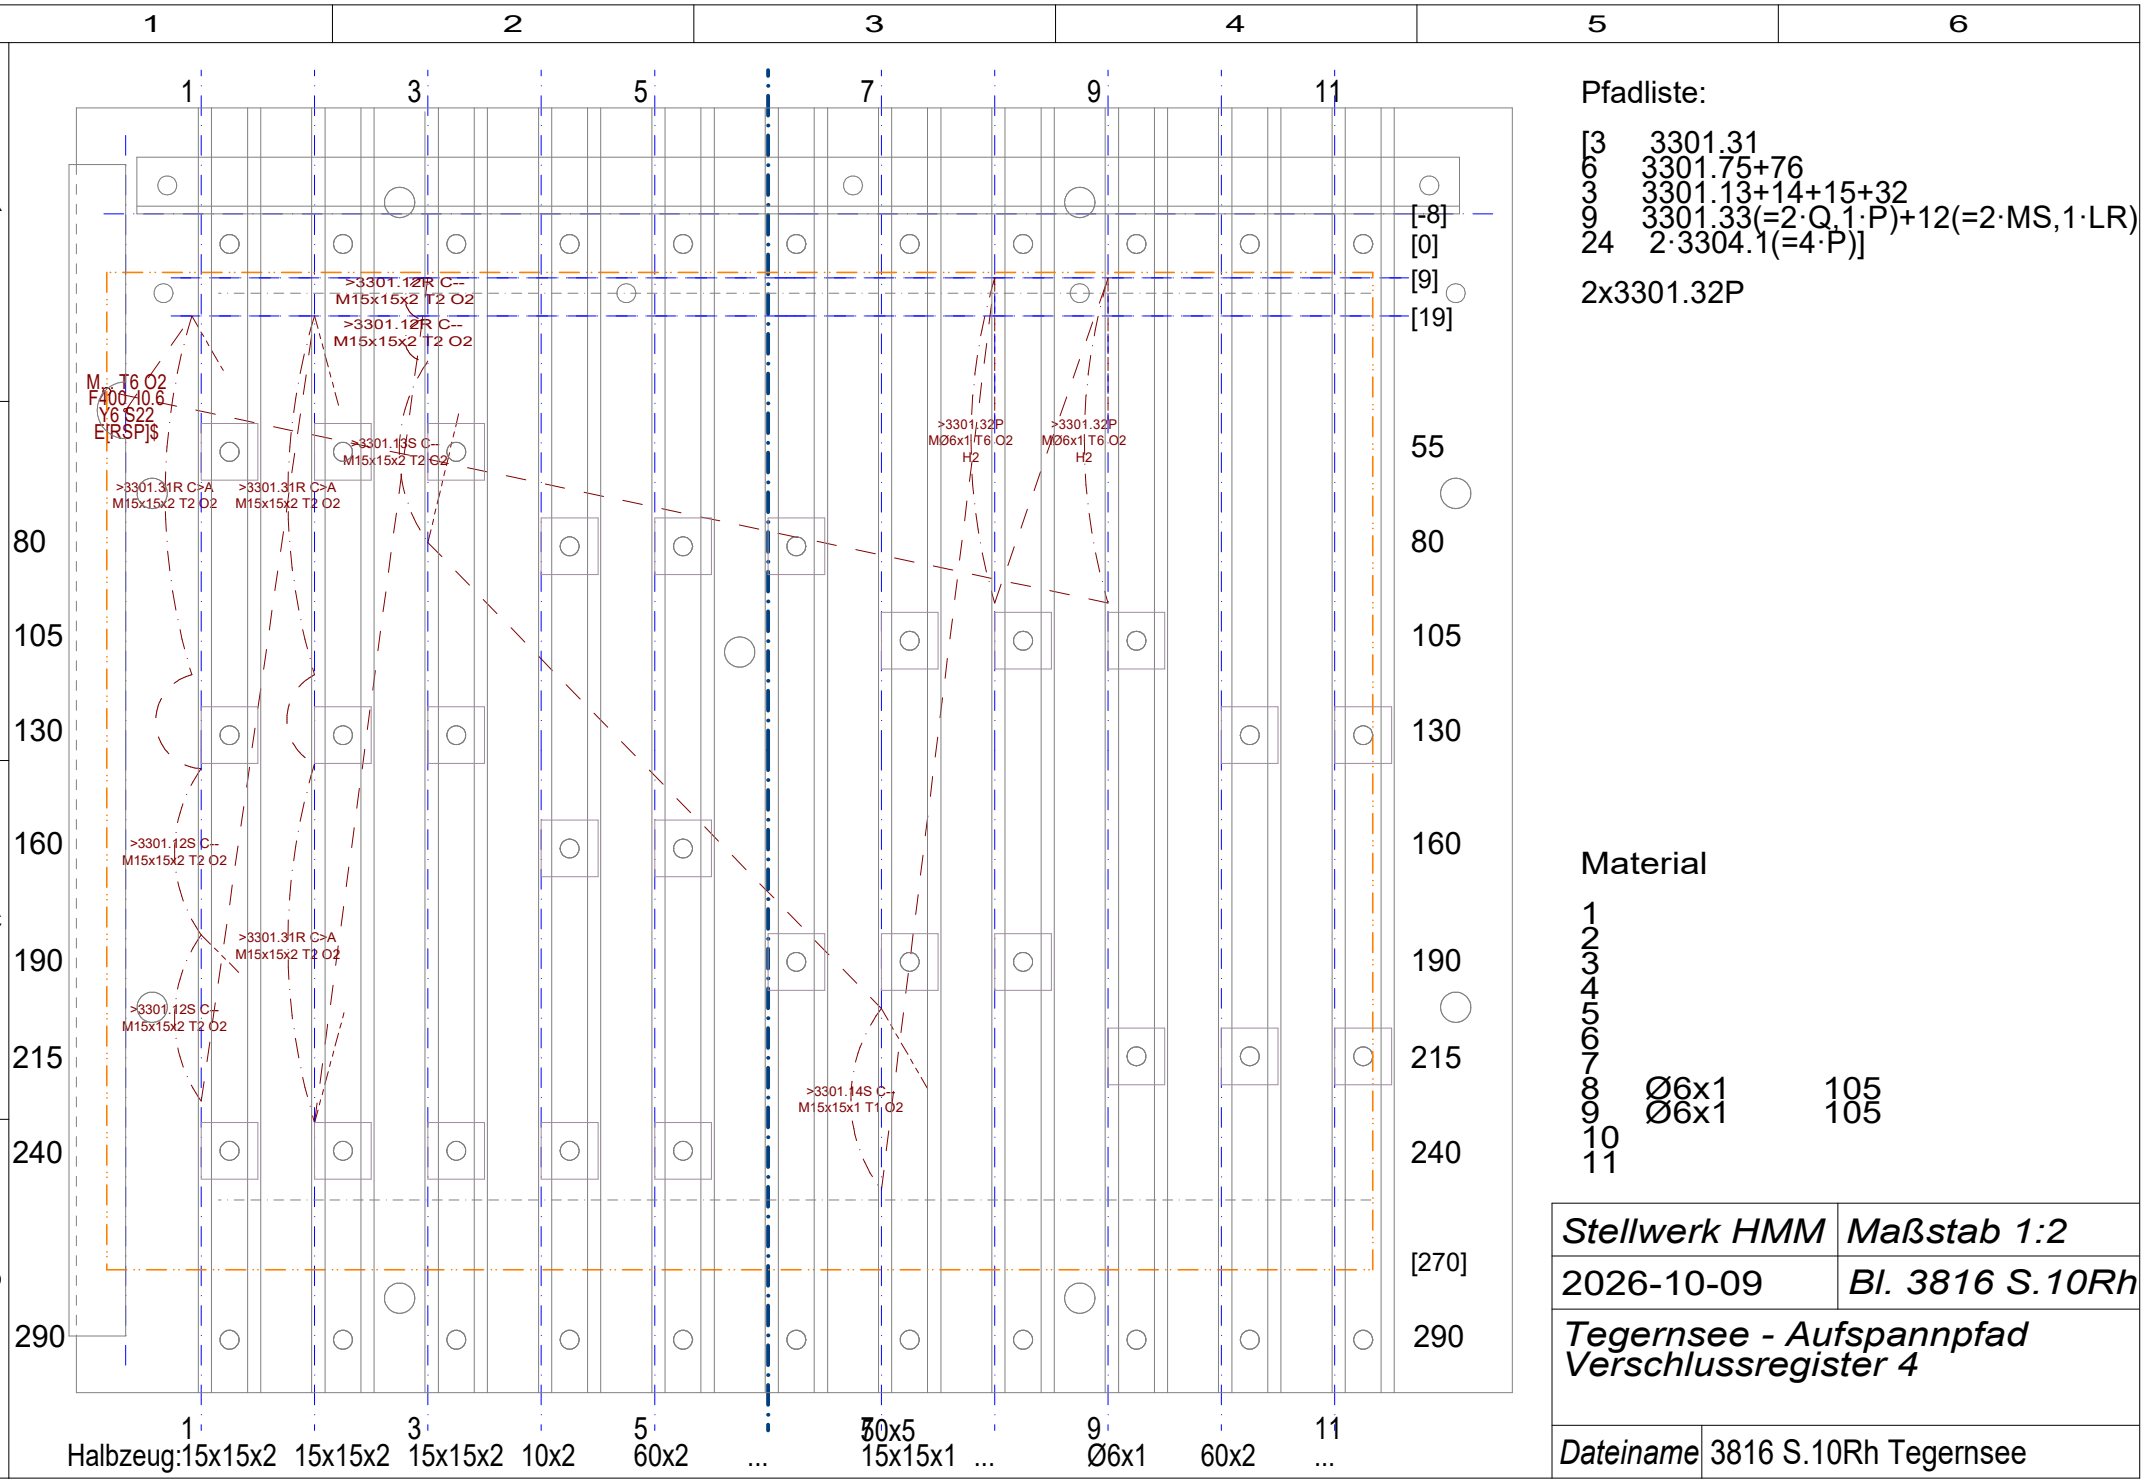


Pfadliste:

[3 3301.31
6 3301.75+76
3 3301.13+14+15+32
9 3301.33(=2·Q,1·P)+12(=2·MS,1·LR)
24 2·3304.1(=4·P)]

2x3301.32P

Material

1		
2		
3		
4		
5		
6		
7		
8	Ø6x1	105
9	Ø6x1	105
10		
11		

Stellwerk HMM	*Maßstab 1:2*
2026-10-09	*Bl. 3816 S.10Rh*
Tegernsee - Aufspannpfad Verschlussregister 4	
Dateiname	3816 S.10Rh Tegernsee