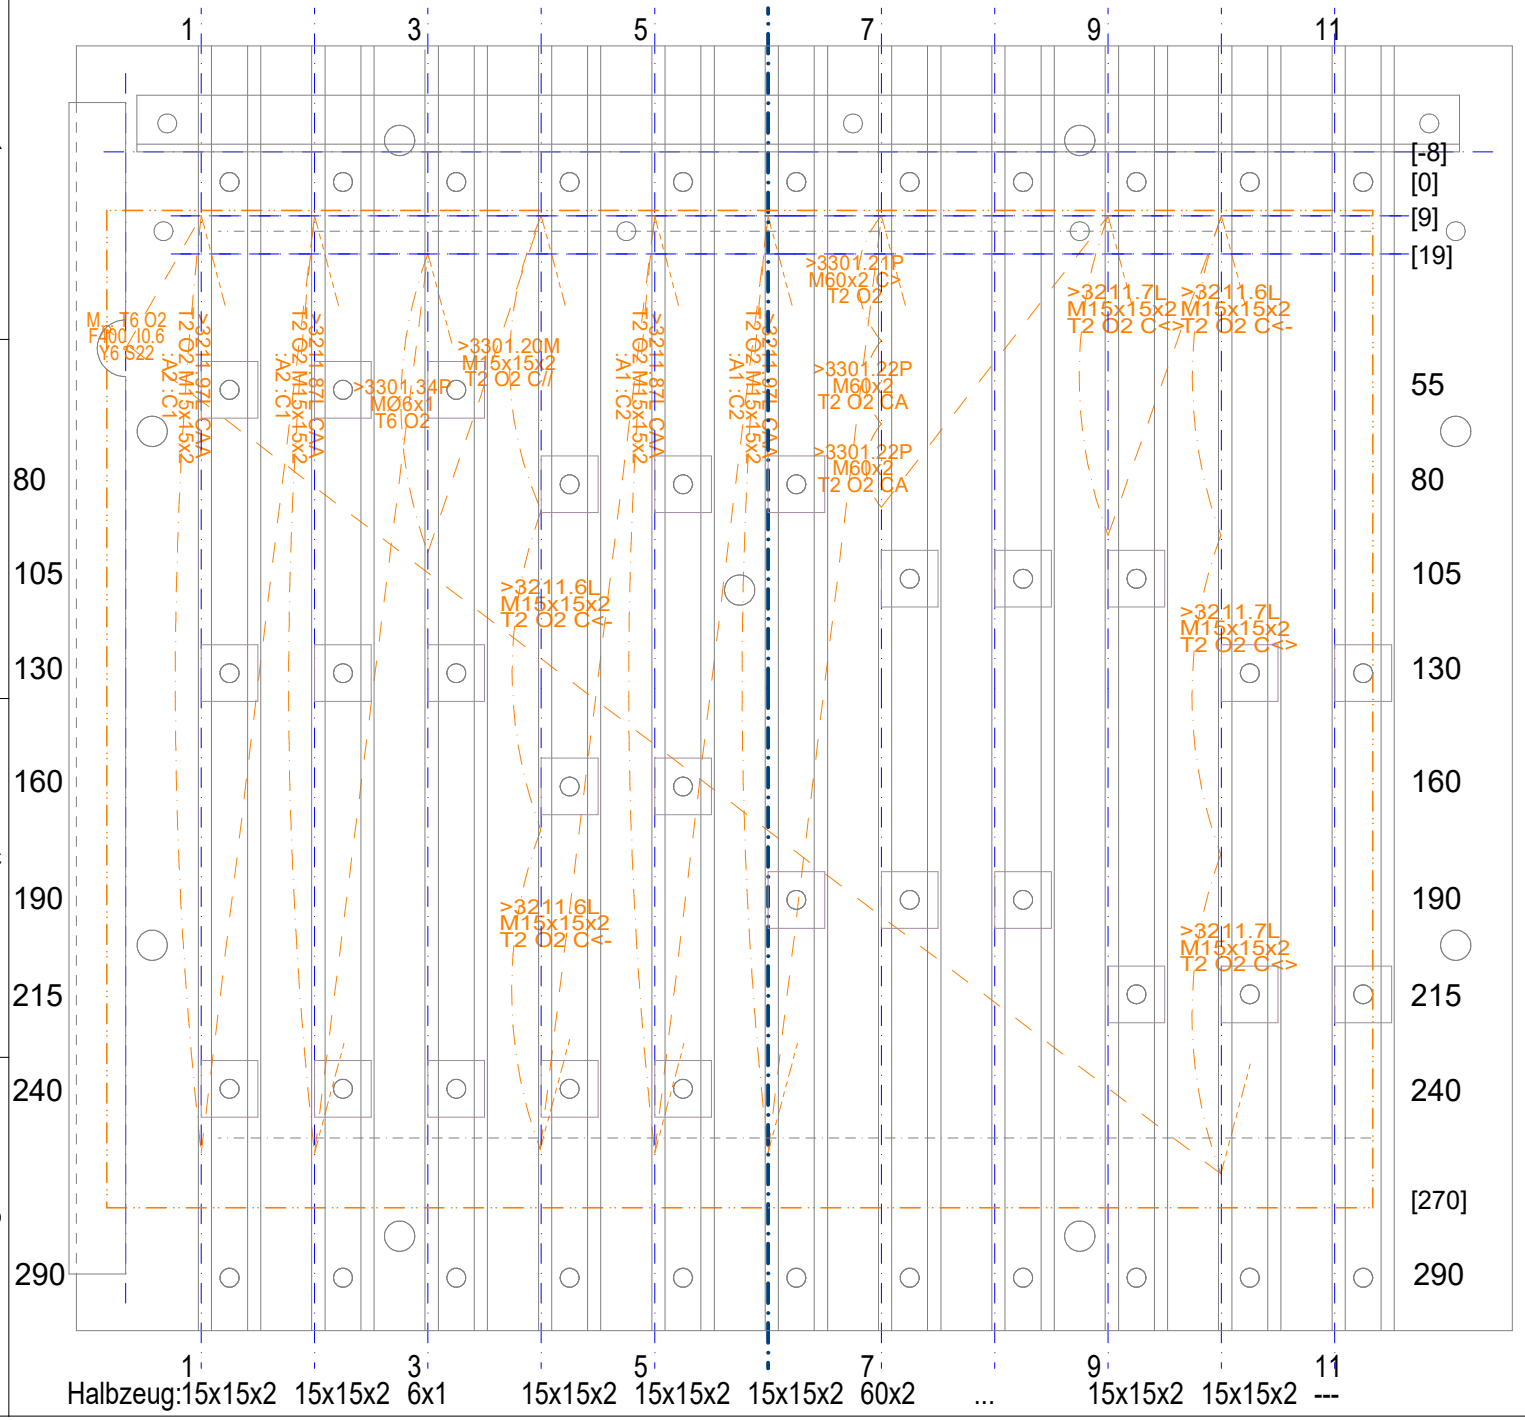


Pfadliste:

[1 3301.21+22+22+24+34+3·20
3 3211.20+21
1 3211.87+97:A2:C1
1 3211.87+97:A1:C2
3 3211.6+7]

ALLE

Material

1	15x15x2	290
2	15x15x2	290
3	6x1	130
4	15x15x2	290
5	15x15x2	290
6	15x15x2	290
7	60x2	105
8		
9	15x15x2	105
10	15x15x2	290
11		

Stellwerk HMM	*Maßstab 1:2*
2026-10-09	*Bl. 3816 S.12Lh*
Tegernsee - Aufspannpfad Verschlussregister 6	
Dateiname	3816 S.12Lh Tegernsee