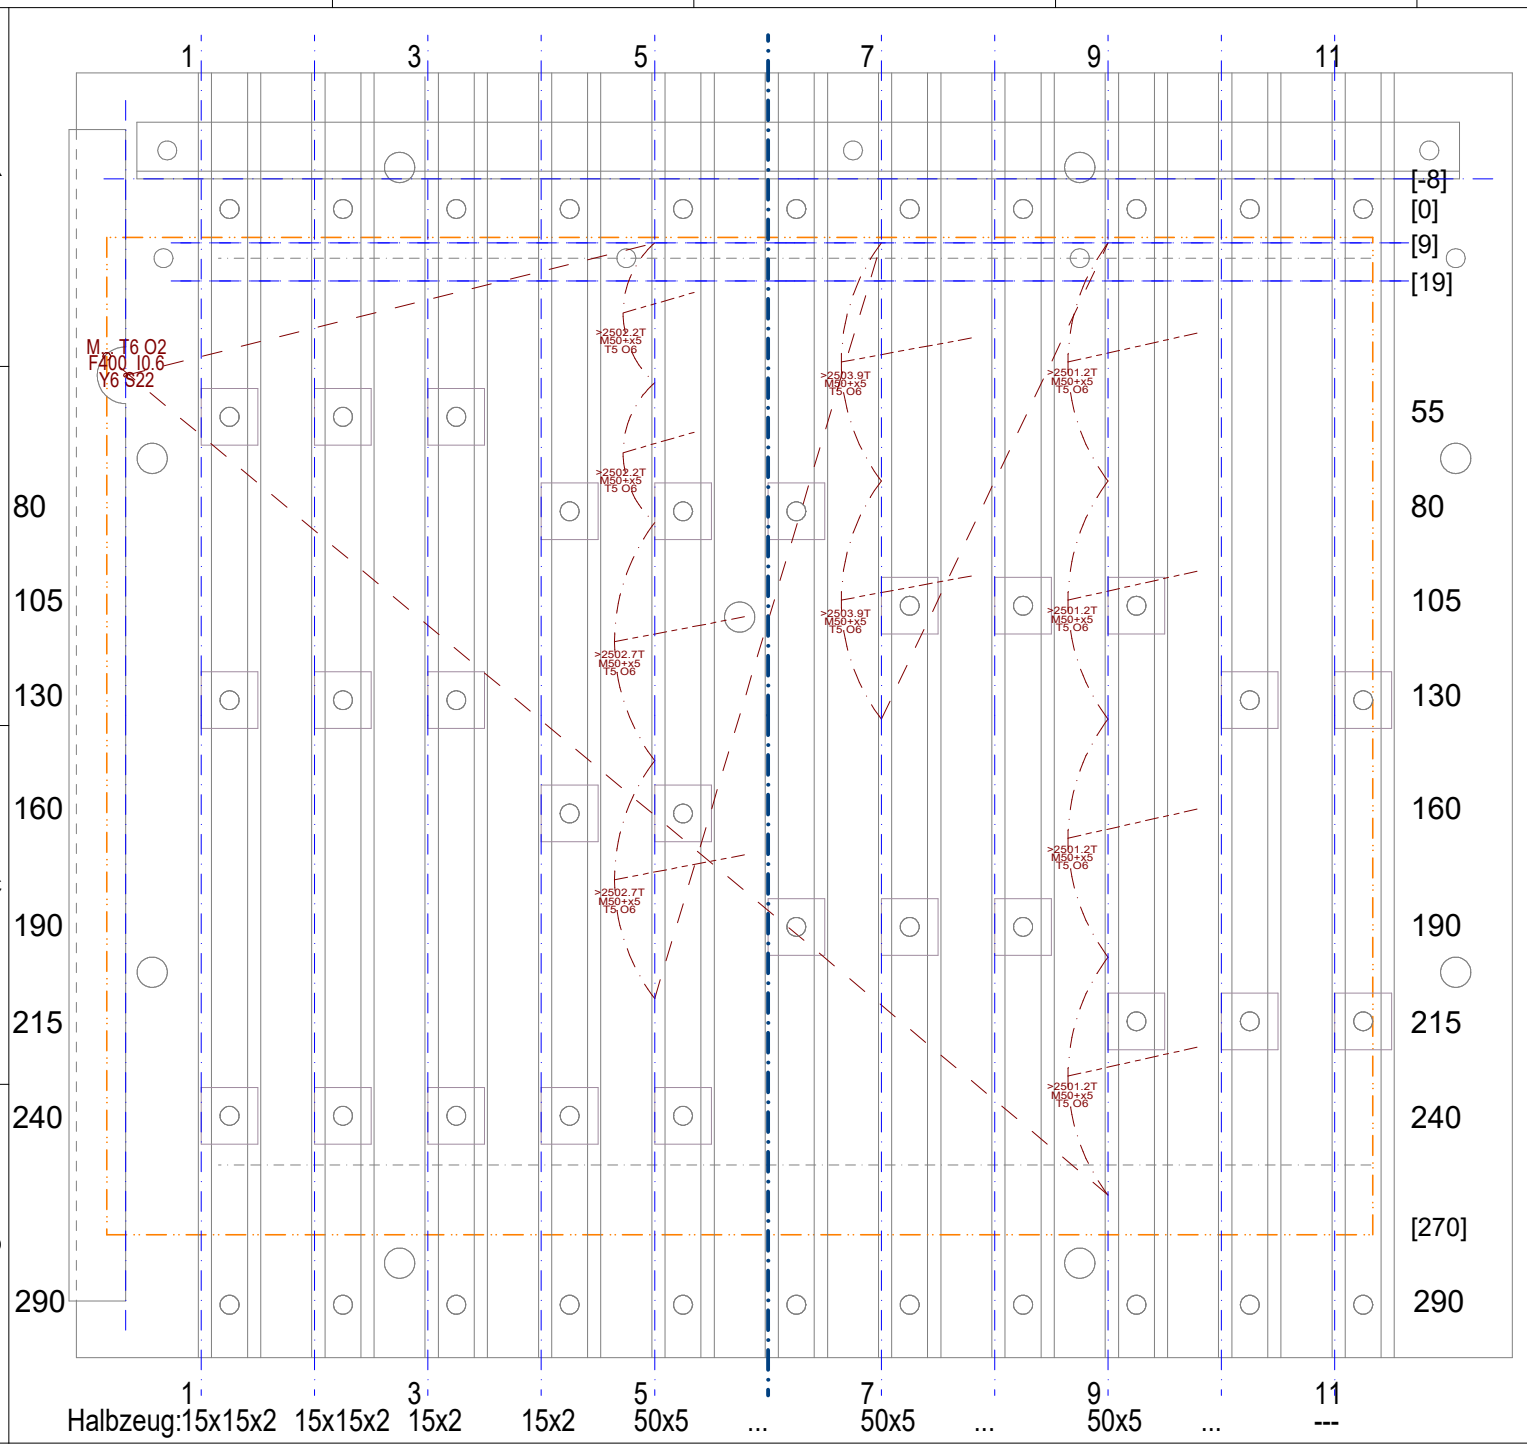


Pfadliste:

[4 2501.1+2+3+4+5
2 2·(2501.1+5)
2 2502.1+2+7+10+11
2 2503.2+3+9]

8x2501.1
4x2501.2
2x2501.3
(2x2502.1 siehe 11P)
2x2502.2
2x2502.7
2x2503.2
2x2503.9

(fehlt noch: 4x2501.1, 2x2501.3)

Material

1	15x15x2	290
2	15x15x2	290
3	15x2	240
4	15x2	240
5	50x5	240
6		
7	50x5	190
8		
9	50x5	290
10		
11		

Stellwerk HMM	*Maßstab 1:2*
2026-10-09	*Bl. 3816 S.13Th*
Tegernsee - Aufspannpfad Abtriebe 1	
Dateiname	3816 S.13Th Tegernsee