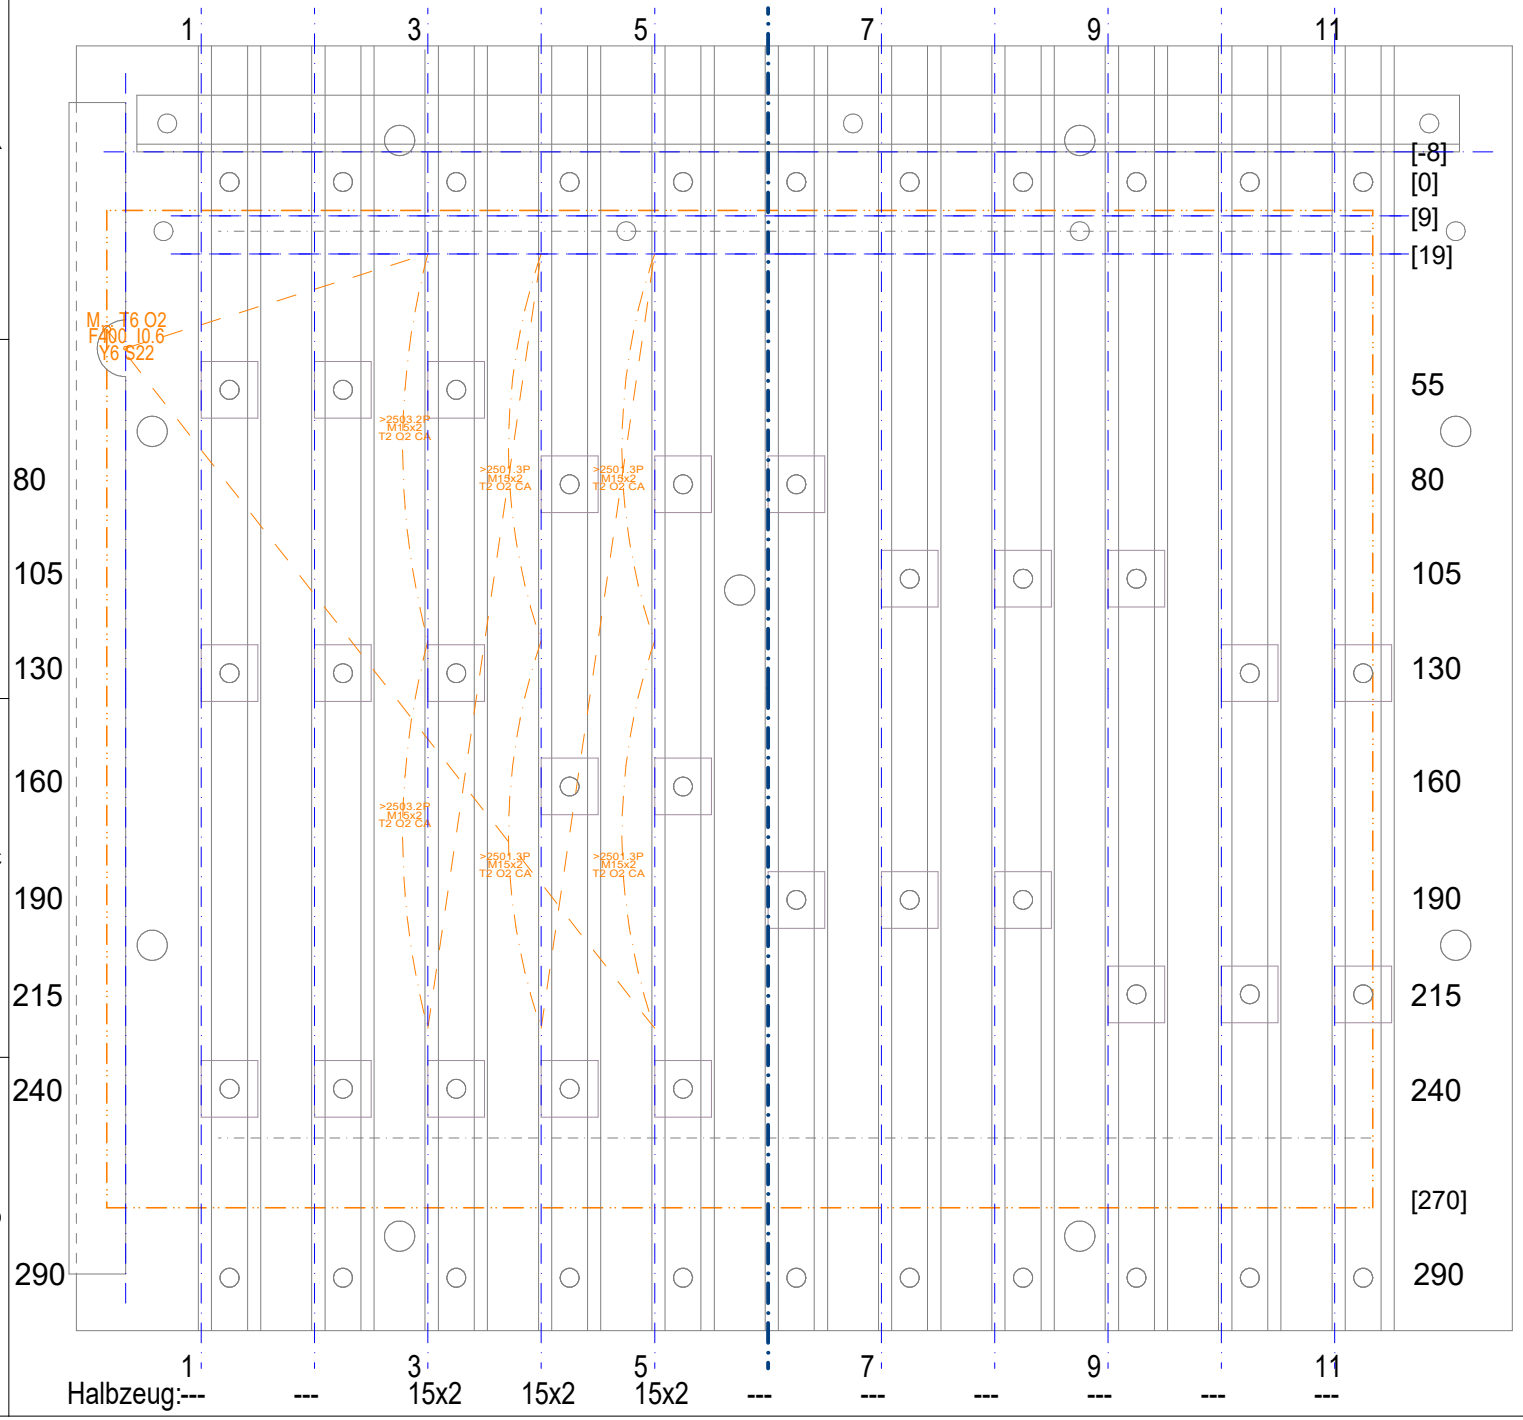


Pfadliste:

[4 2501.1+2+3+4+5
2 2·(2501.1+5)
2 2502.1+2+7+10+11
2 2503.2+3+9]

4x2501.4
2x2501.3

Material

1		
2		
3	15x2	240
4	15x2	240
5	15x2	240
6		
7		
8		
9		
10		
11		

Stellwerk HMM	*Maßstab 1:2*
2026-10-09	*Bl. 3816 S.14Ph*
Tegernsee - Aufspannpfad Abtriebe 2	
Dateiname	3816 S.14Ph Tegernsee