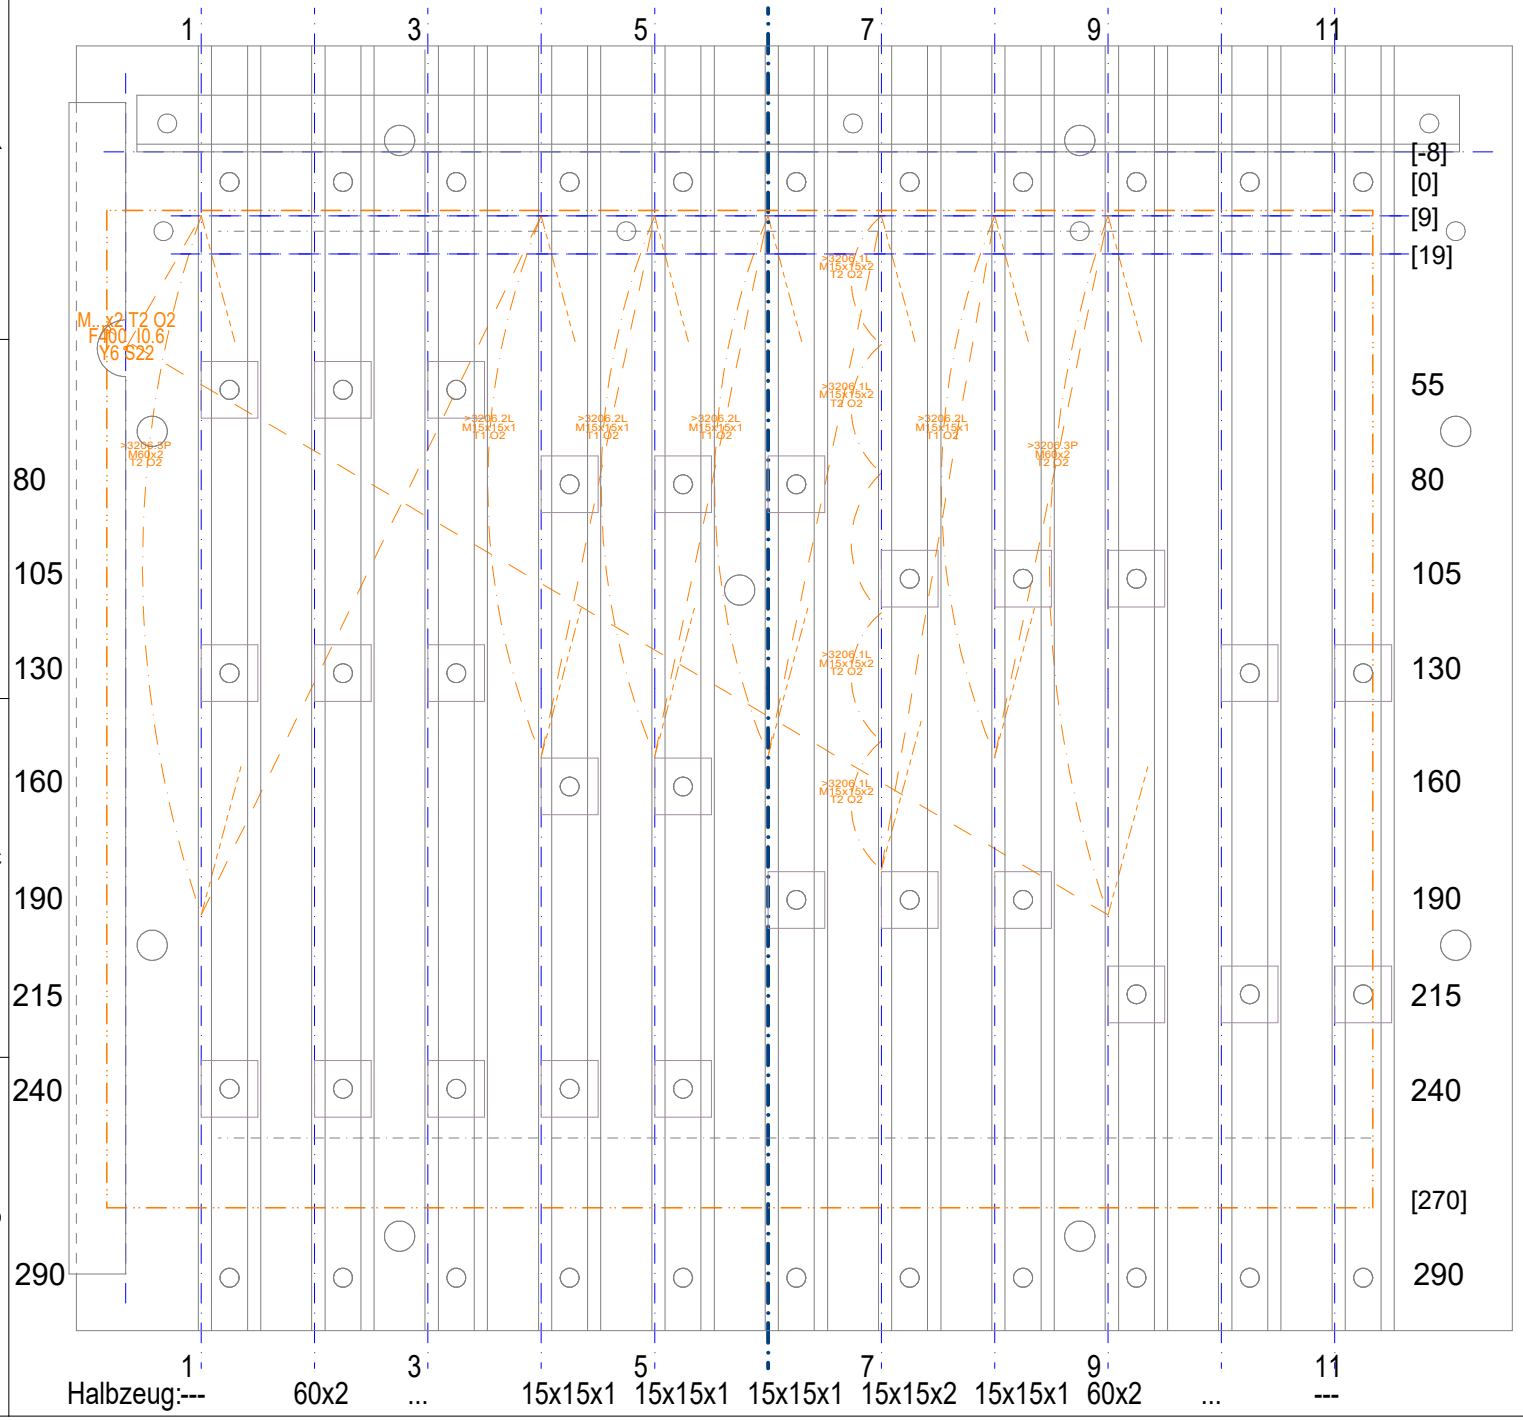


Pfadliste:

[4 X 3206.1+2+3+4+5]
4 3206.1L+2L
2 3206.3P

Material

1		
2	60x2	240
3		
4	15x15x1	160
5	15x15x1	160
6	15x15x1	190
7	15x15x2	190/105
8	15x15x1	190
9	60x2	215
10		

Stellwerk HMM	*Maßstab 1:2*
2026-09-25	*Bl. 3816 S.2LPh*
Tegernsee - Aufspannpfad Hebel 1	
Dateiname	3816 S.2LPh Tegernsee