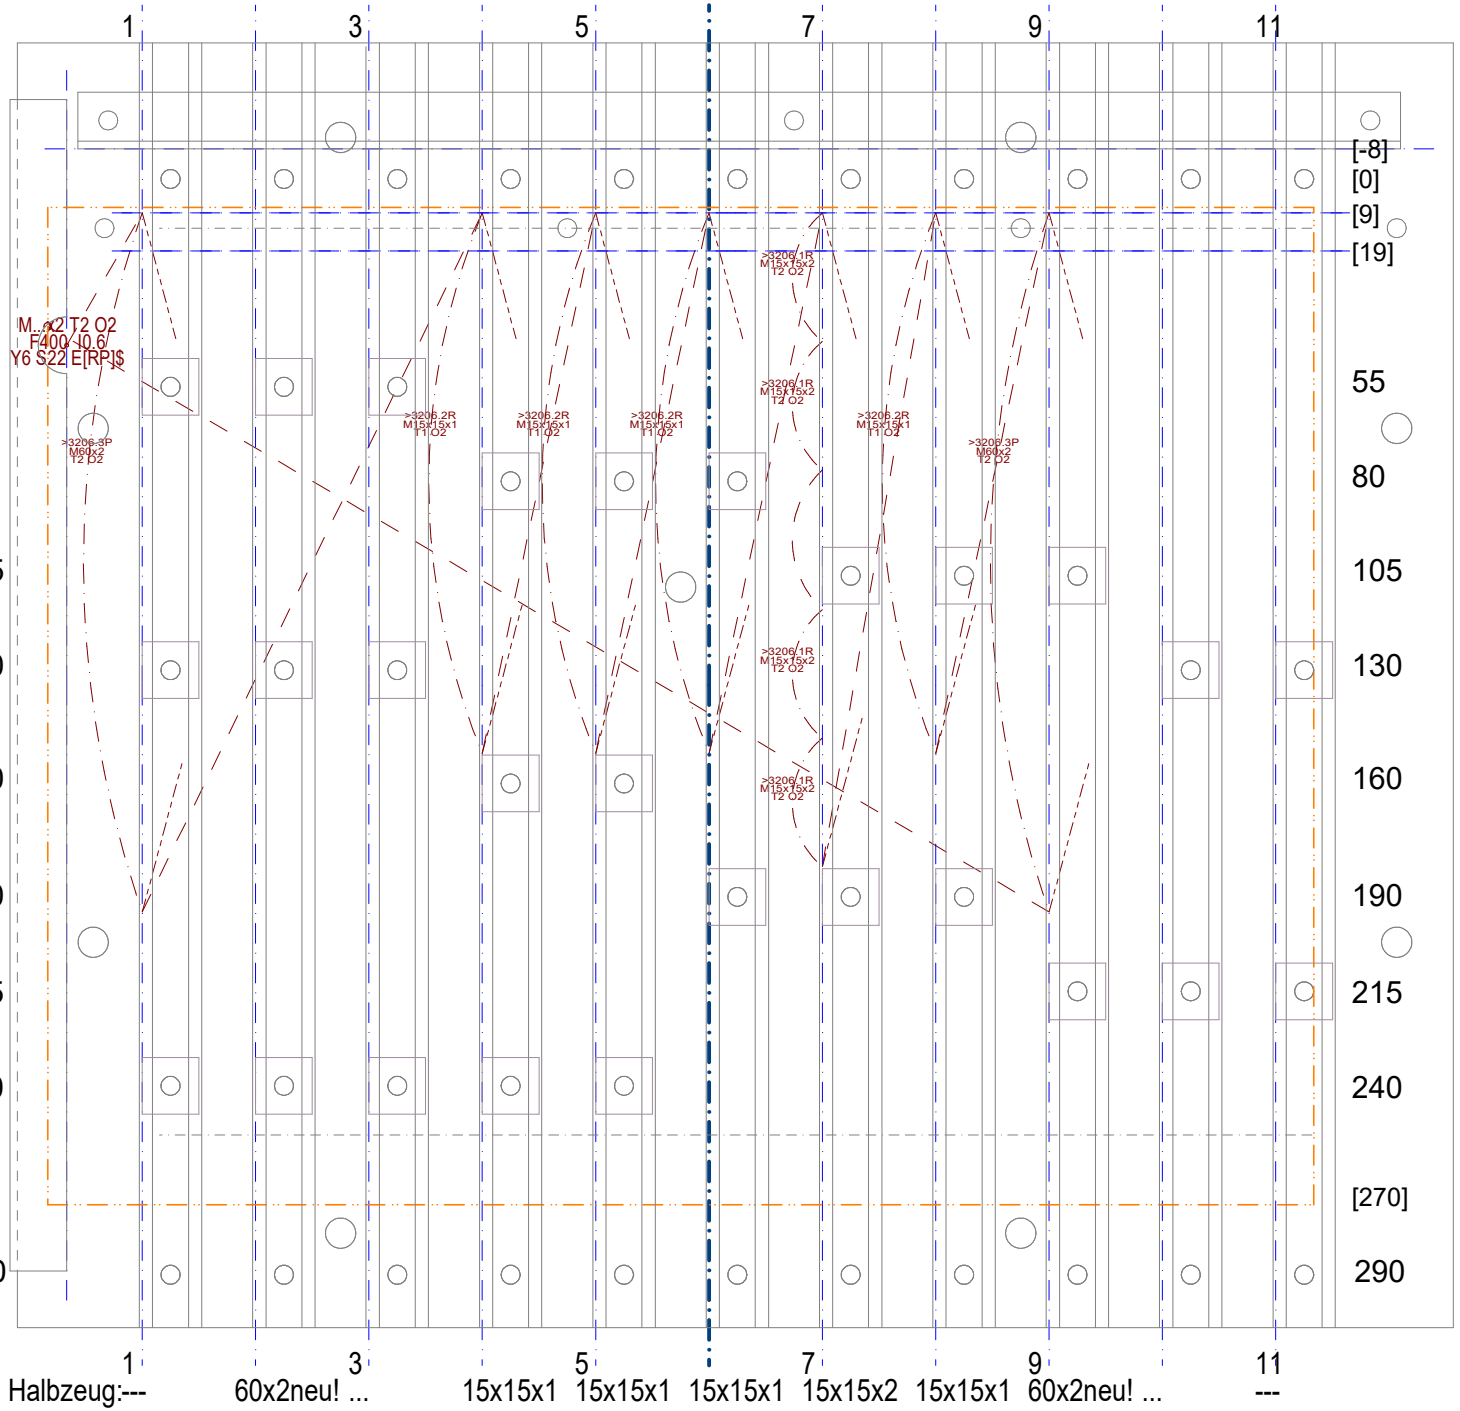


Pfadliste:

[4 X 3206.1+2+3+4+5]
4 3206.1R+2R
2 3206.3P

Material

1		
2	60x2	240
3		
4		
5		
6		
7		
8		
9	60x2	215
10		

Stellwerk HMM	*Maßstab 1:2*
2026-09-25	*Bl. 3816 S.2RPh*
Tegernsee - Aufspannpfad Hebel 1	
Dateiname	3816 S.2RPh Tegernsee