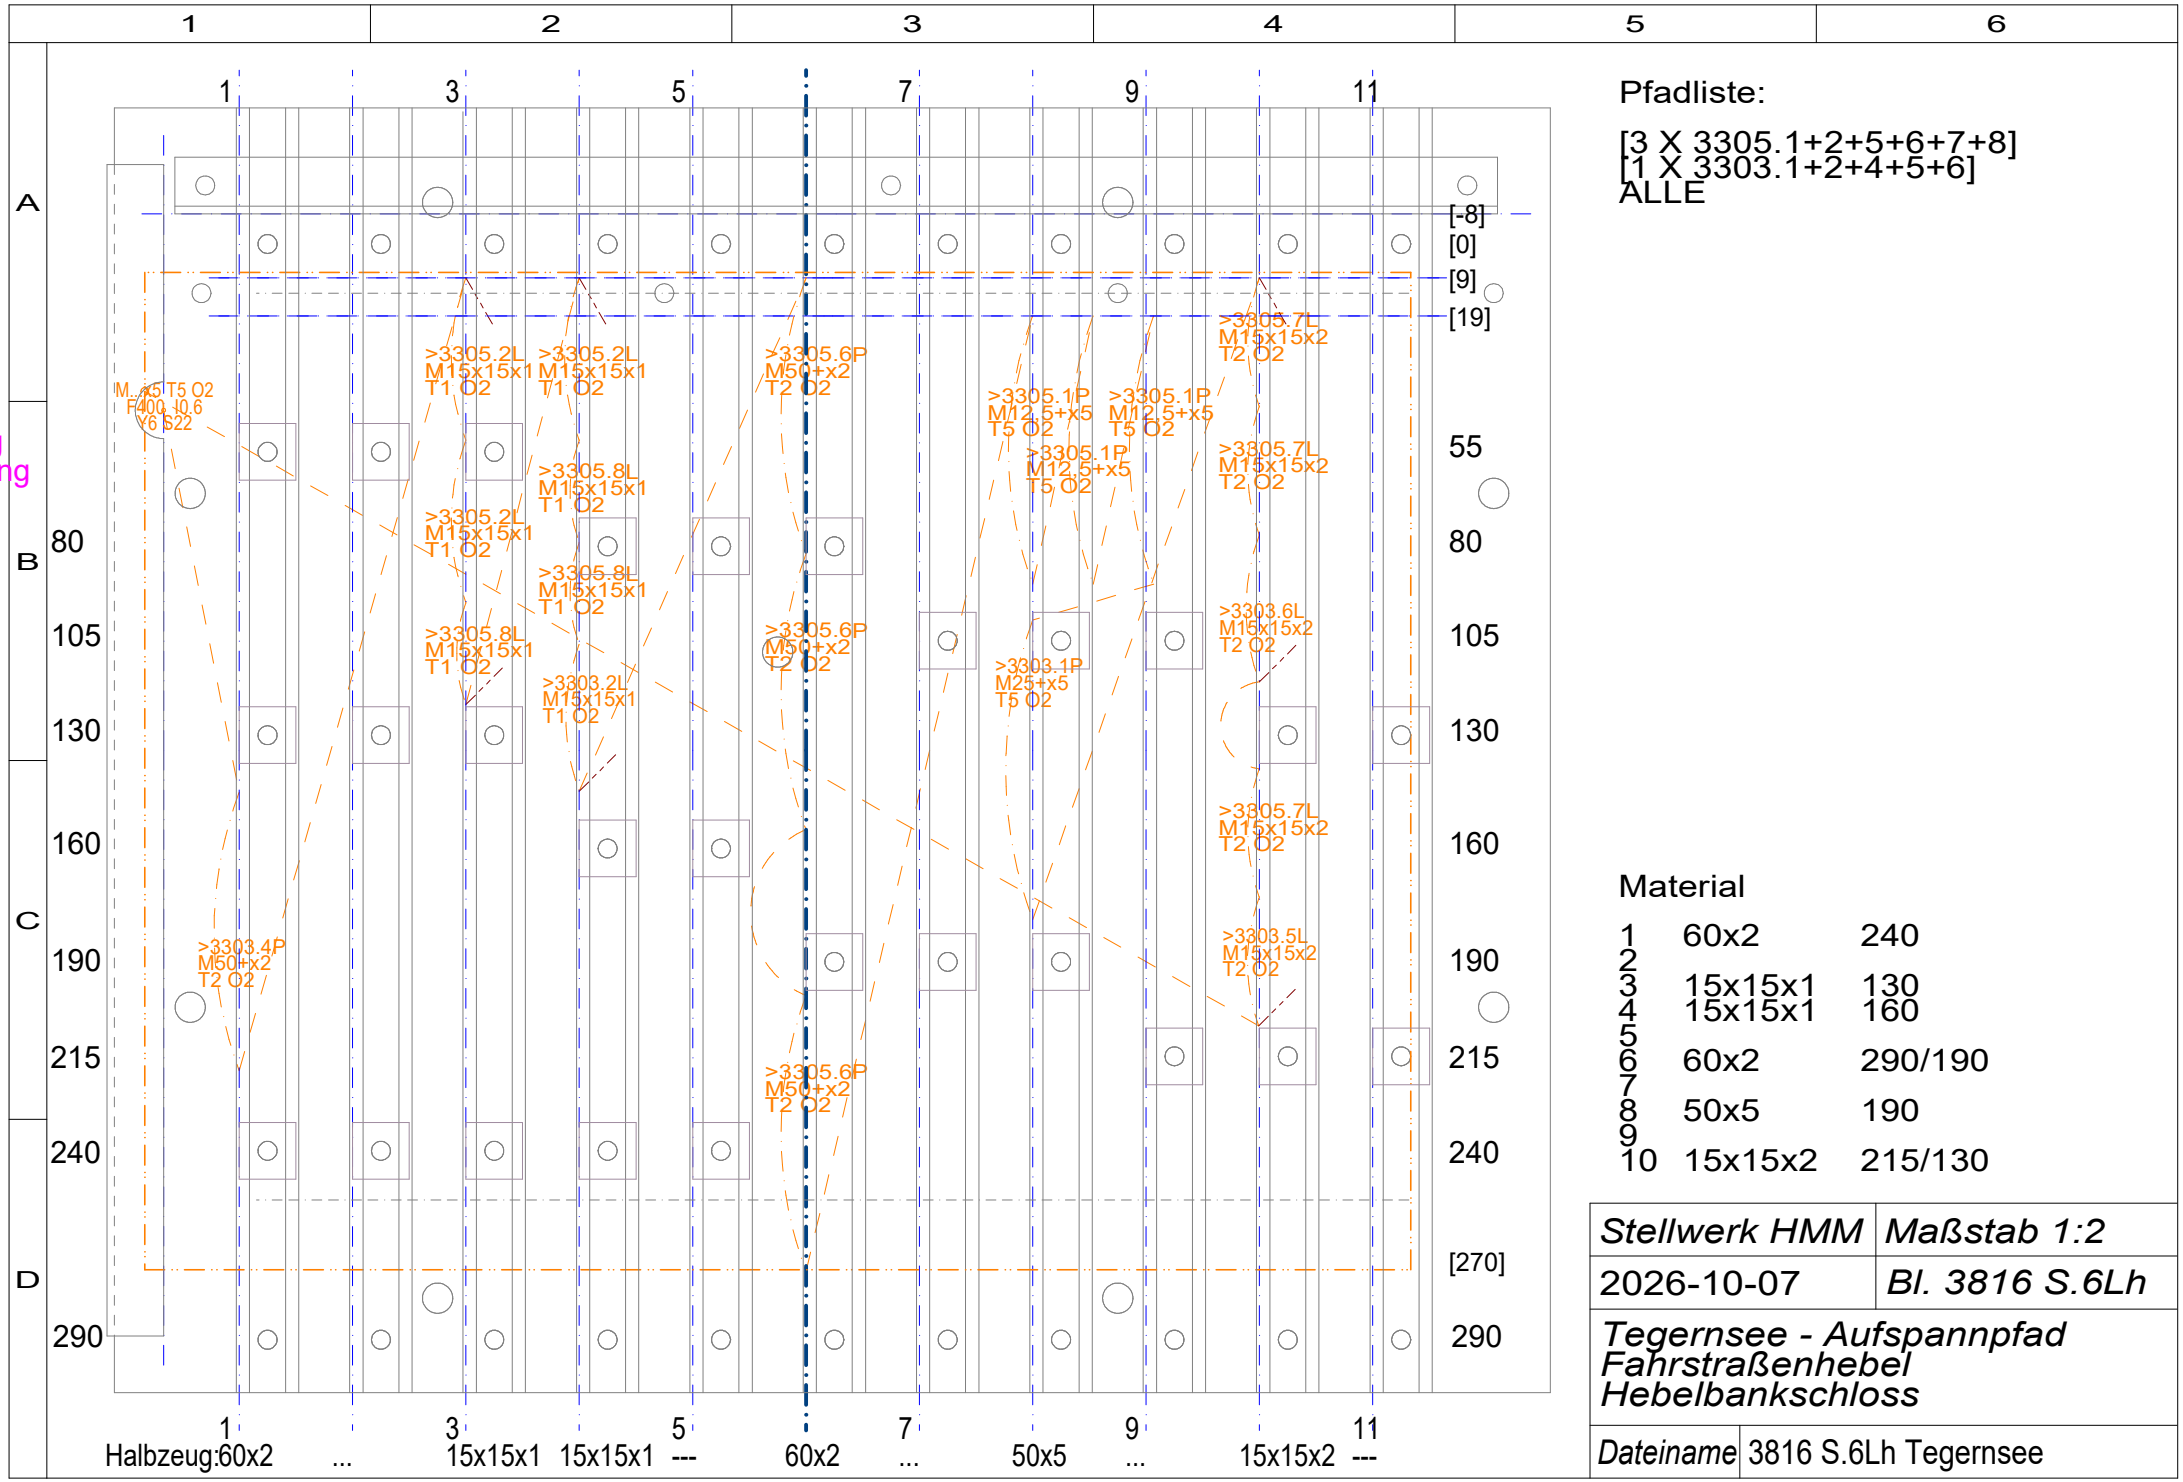


Pfadliste:

[3 X 3305.1+2+5+6+7+8]
[1 X 3303.1+2+4+5+6]
ALLE

Material

1	60x2	240
2		
3	15x15x1	130
4	15x15x1	160
5		
6	60x2	290/190
7		
8	50x5	190
9		
10	15x15x2	215/130

Stellwerk HMM	*Maßstab 1:2*
2026-10-07	*Bl. 3816 S.6Lh*
Tegernsee - Aufspannpfad Fahrstraßenhebel Hebelbankschloss	
Dateiname	3816 S.6Lh Tegernsee