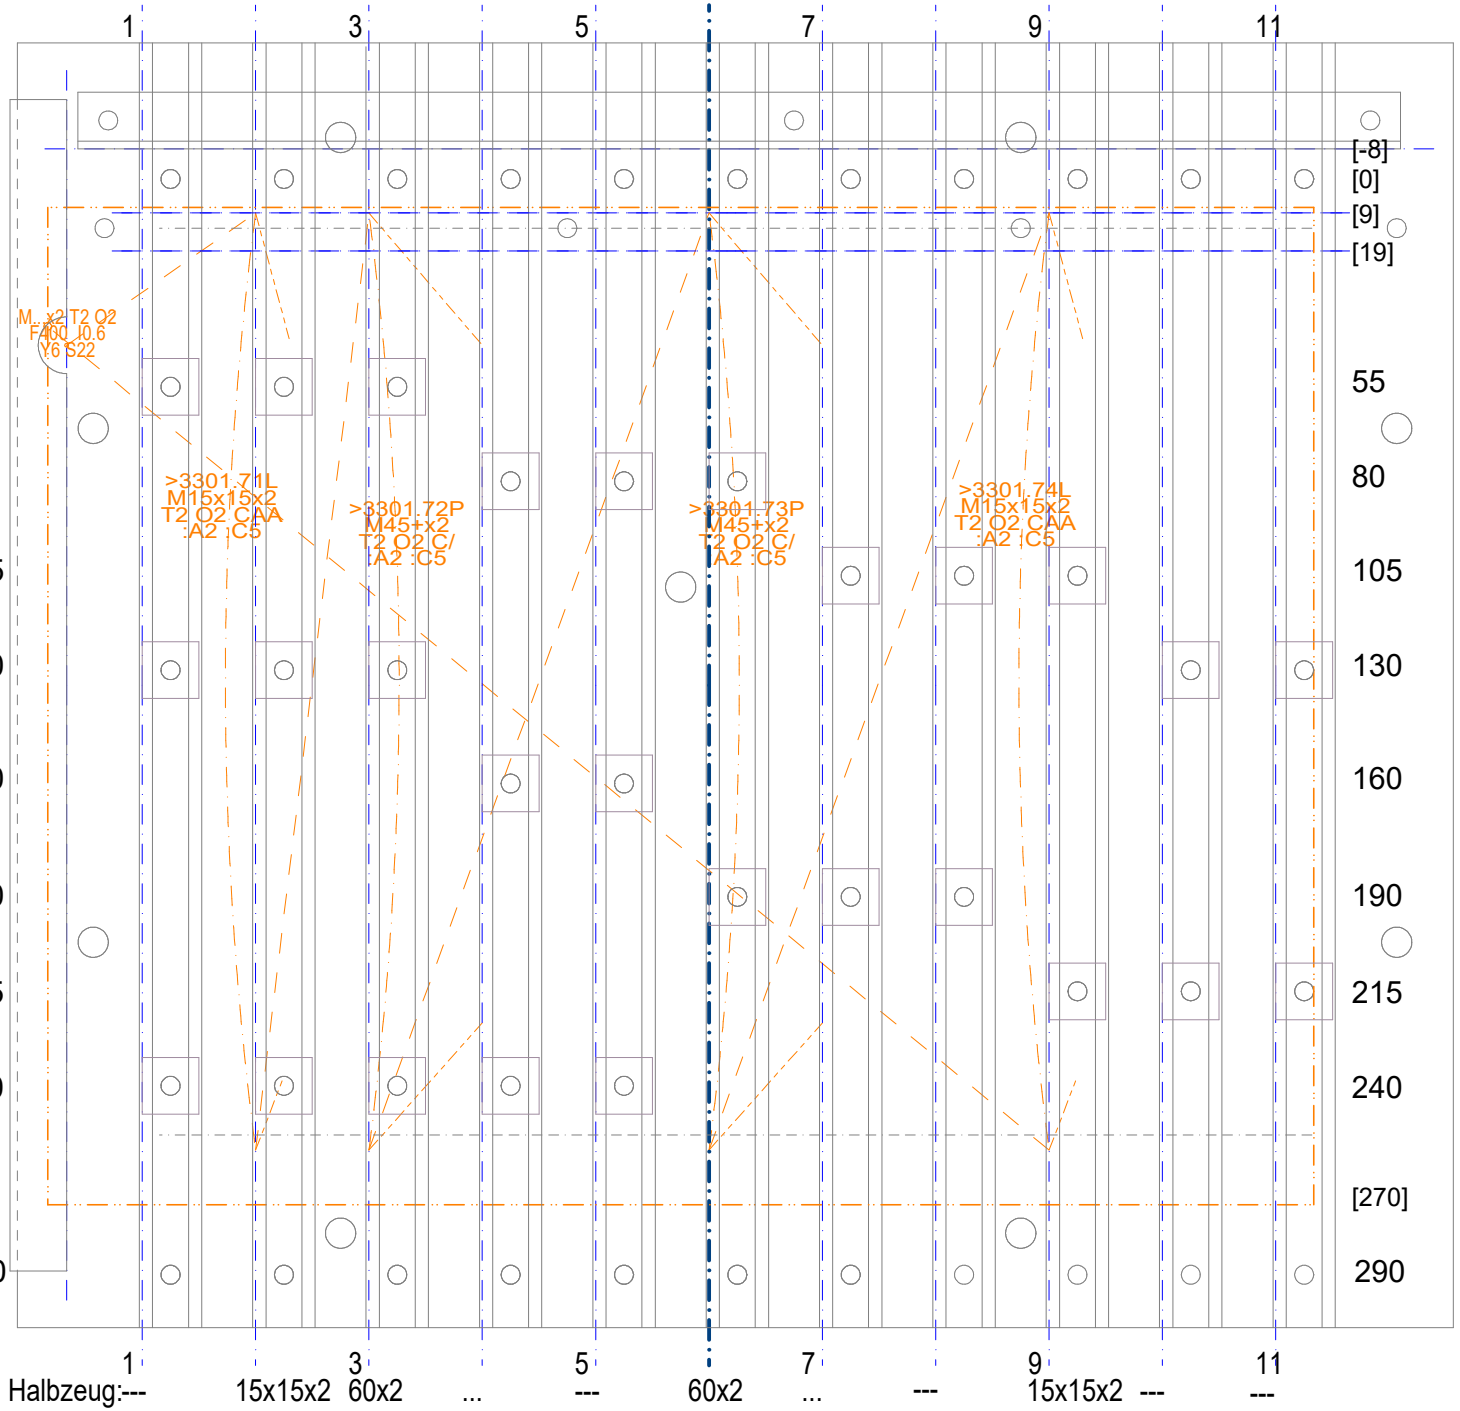


Pfadliste:

[3301.71+72+73+74:A2:C5]
ALLE

Material

1	15x15x2	290
2	60x2	290
3		
4		
5	60x2	290
6		
7		
8	15x15x2	290
9		
10		

Stellwerk HMM	*Maßstab 1:2*
2026-10-08	*Bl. 3816 S.8Lh*
Tegernsee - Aufspannpfad Verschlussregister 2	
Dateiname	3816 S.8Lh Tegernsee