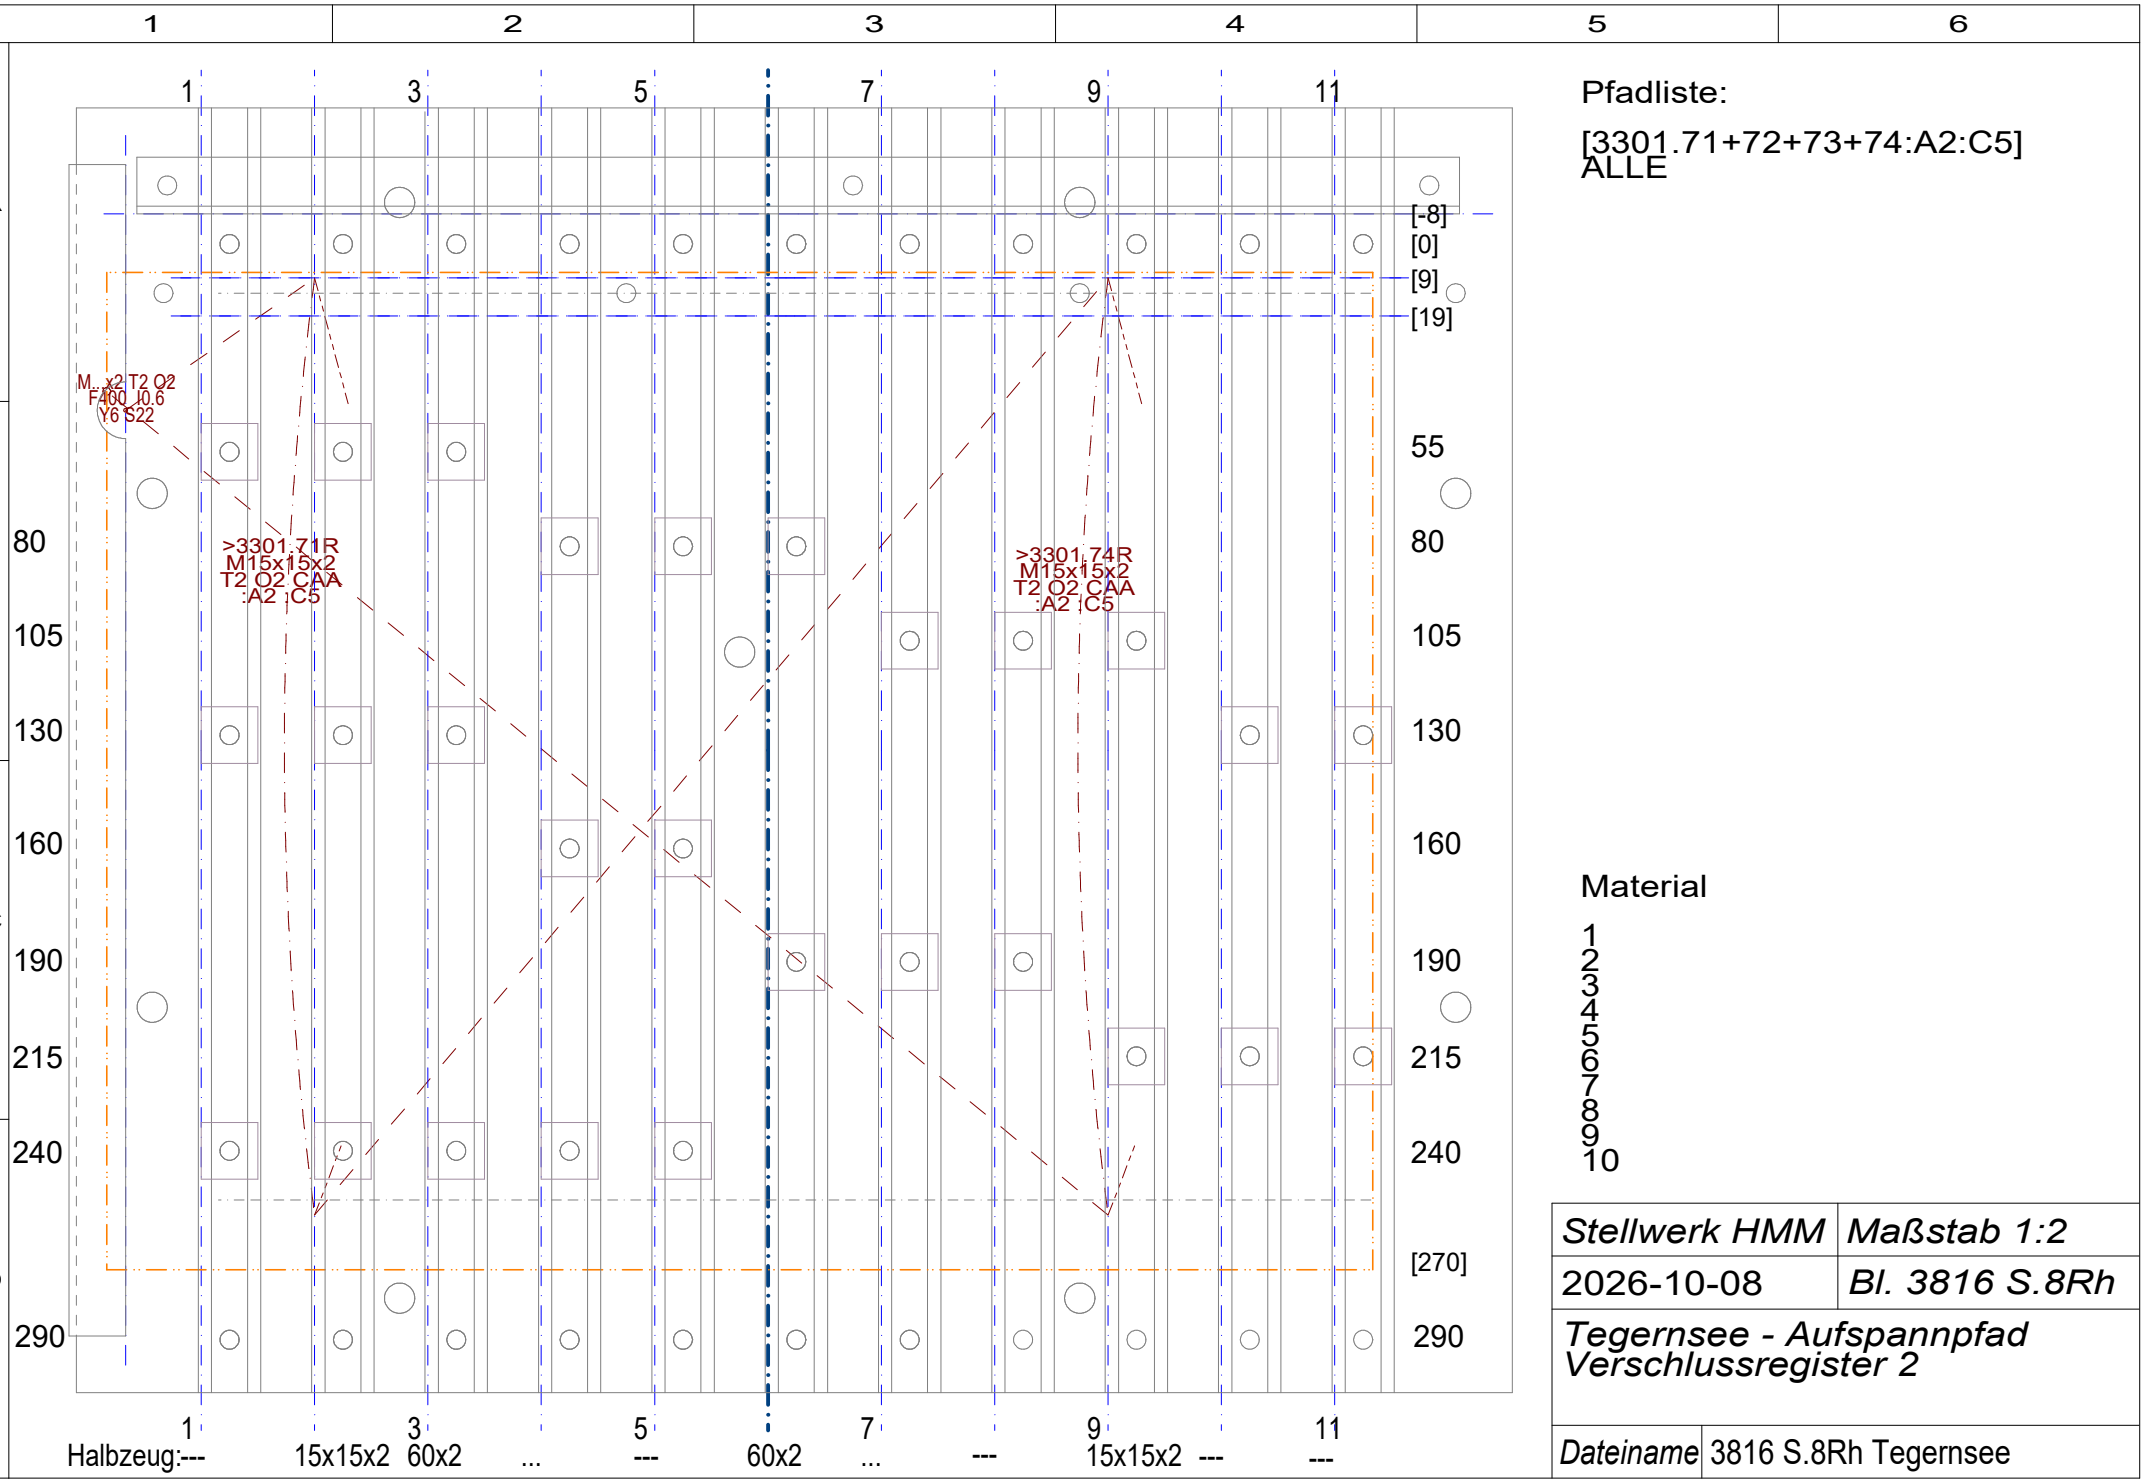


Pfadliste:

[3301.71+72+73+74:A2:C5]
ALLE

Material

1
2
3
4
5
6
7
8
9
10

Stellwerk HMM	*Maßstab 1:2*
2026-10-08	*Bl. 3816 S.8Rh*
Tegernsee - Aufspannpfad Verschlussregister 2	
Dateiname	3816 S.8Rh Tegernsee