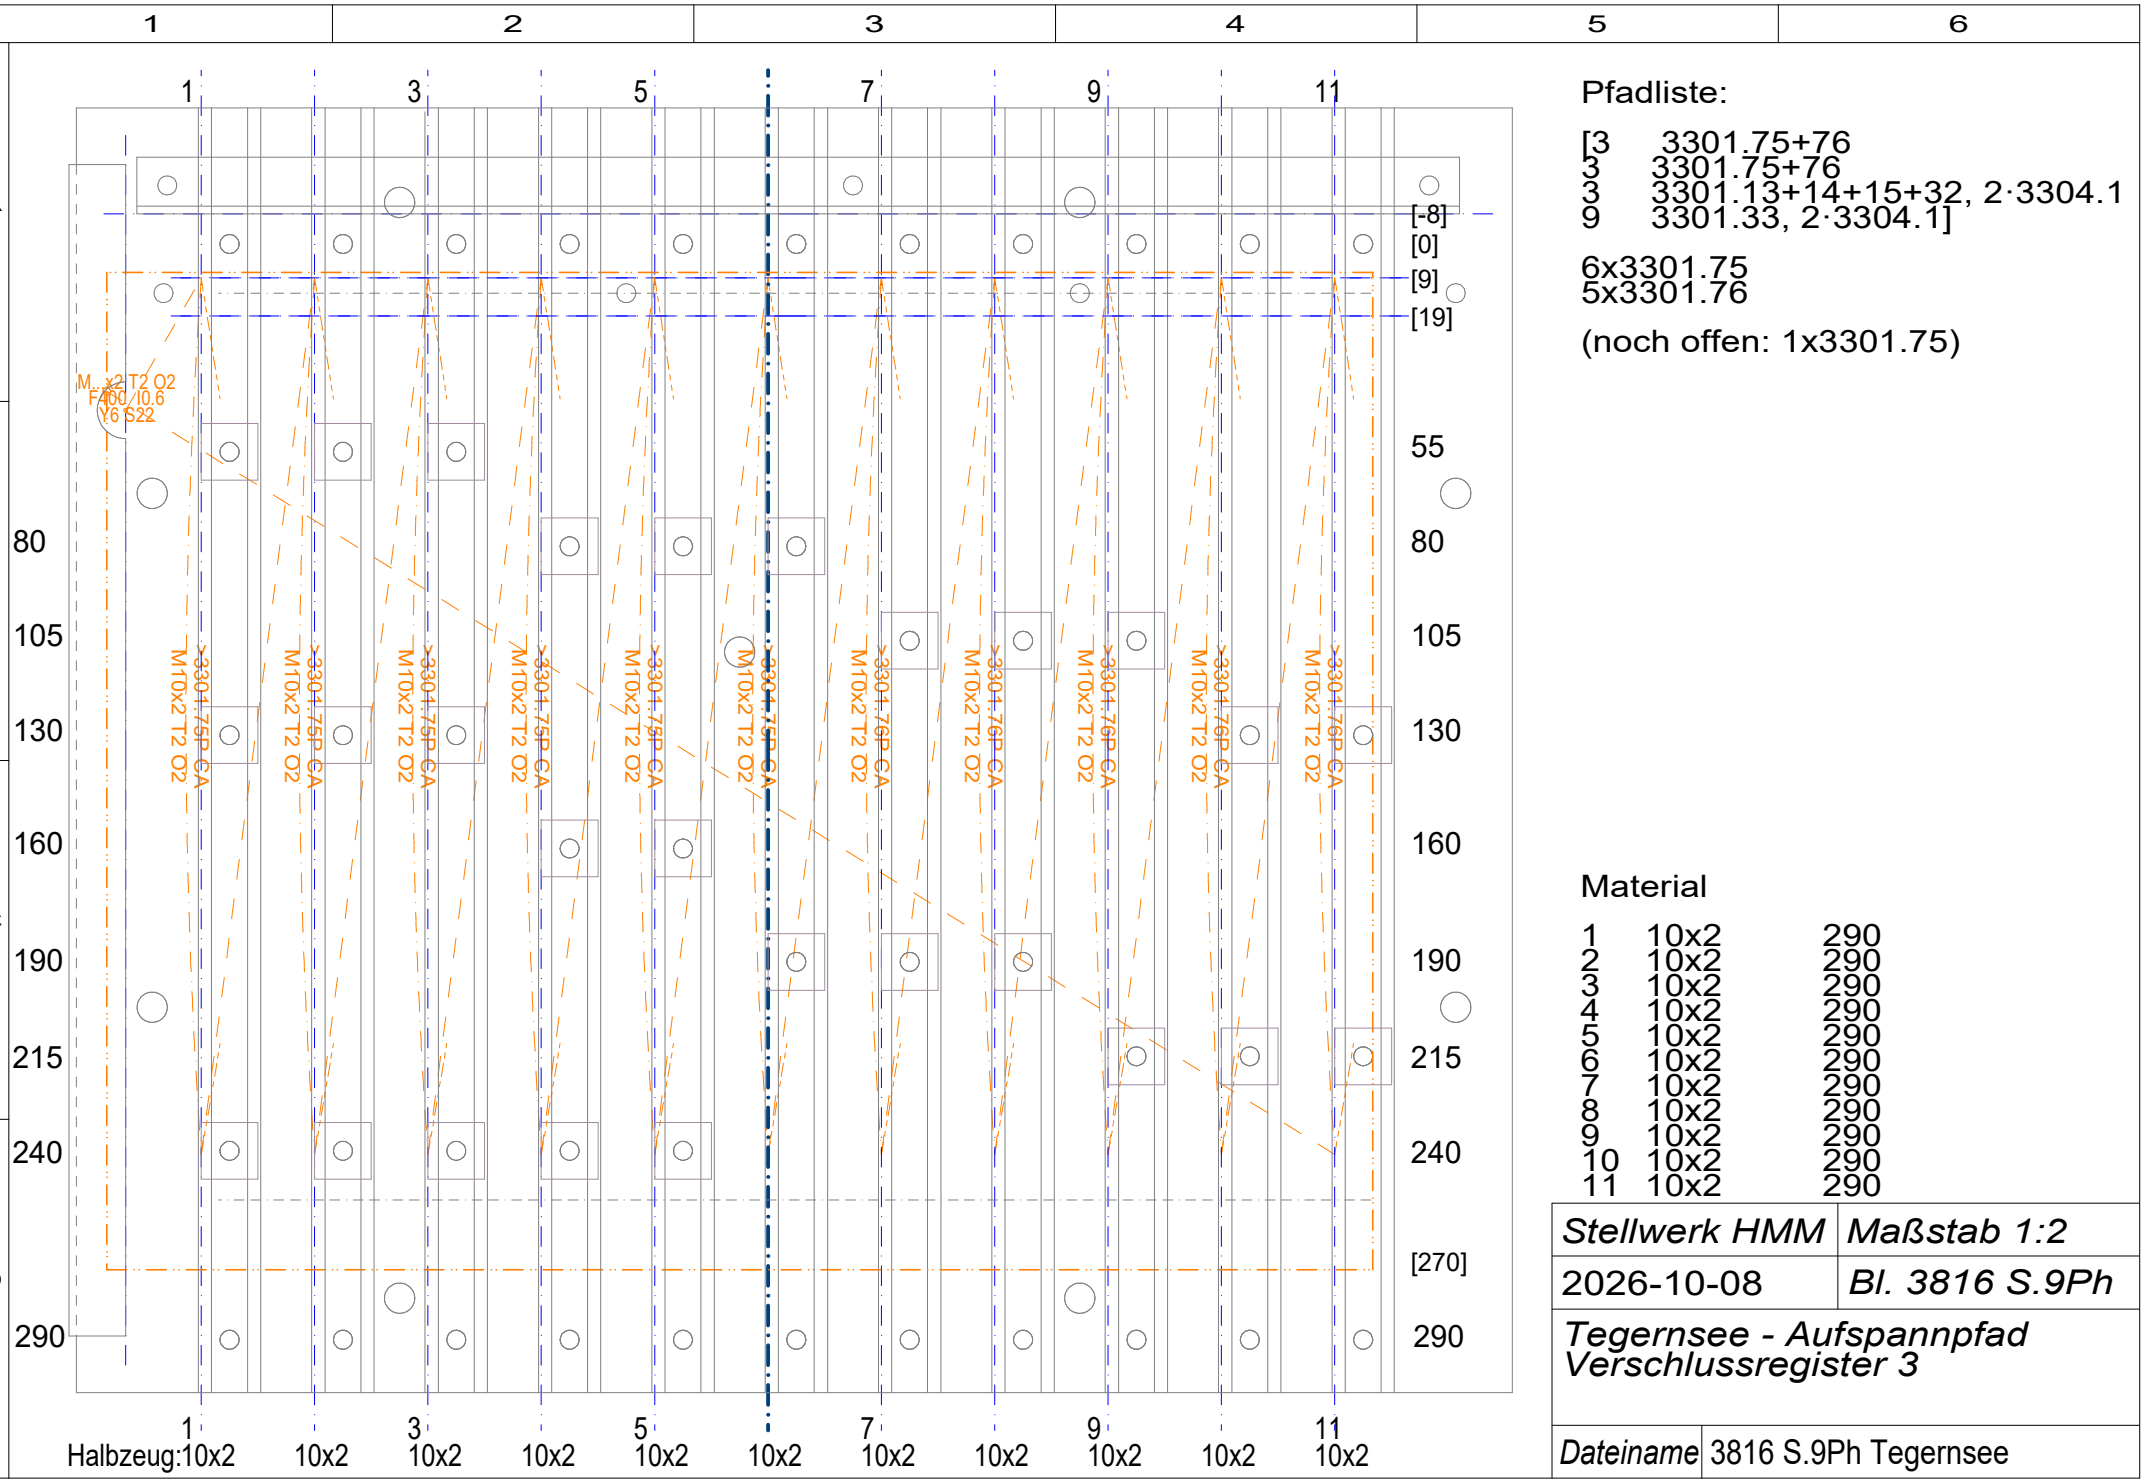


Pfadliste:

[3 3301.75+76
3 3301.75+76
3 3301.13+14+15+32, 2·3304.1
9 3301.33, 2·3304.1]

6x3301.75
5x3301.76

(noch offen: 1x3301.75)

Material

1	10x2	290
2	10x2	290
3	10x2	290
4	10x2	290
5	10x2	290
6	10x2	290
7	10x2	290
8	10x2	290
9	10x2	290
10	10x2	290
11	10x2	290

Stellwerk HMM	*Maßstab 1:2*
2026-10-08	*Bl. 3816 S.9Ph*
Tegernsee - Aufspannpfad Verschlussregister 3	
Dateiname	3816 S.9Ph Tegernsee