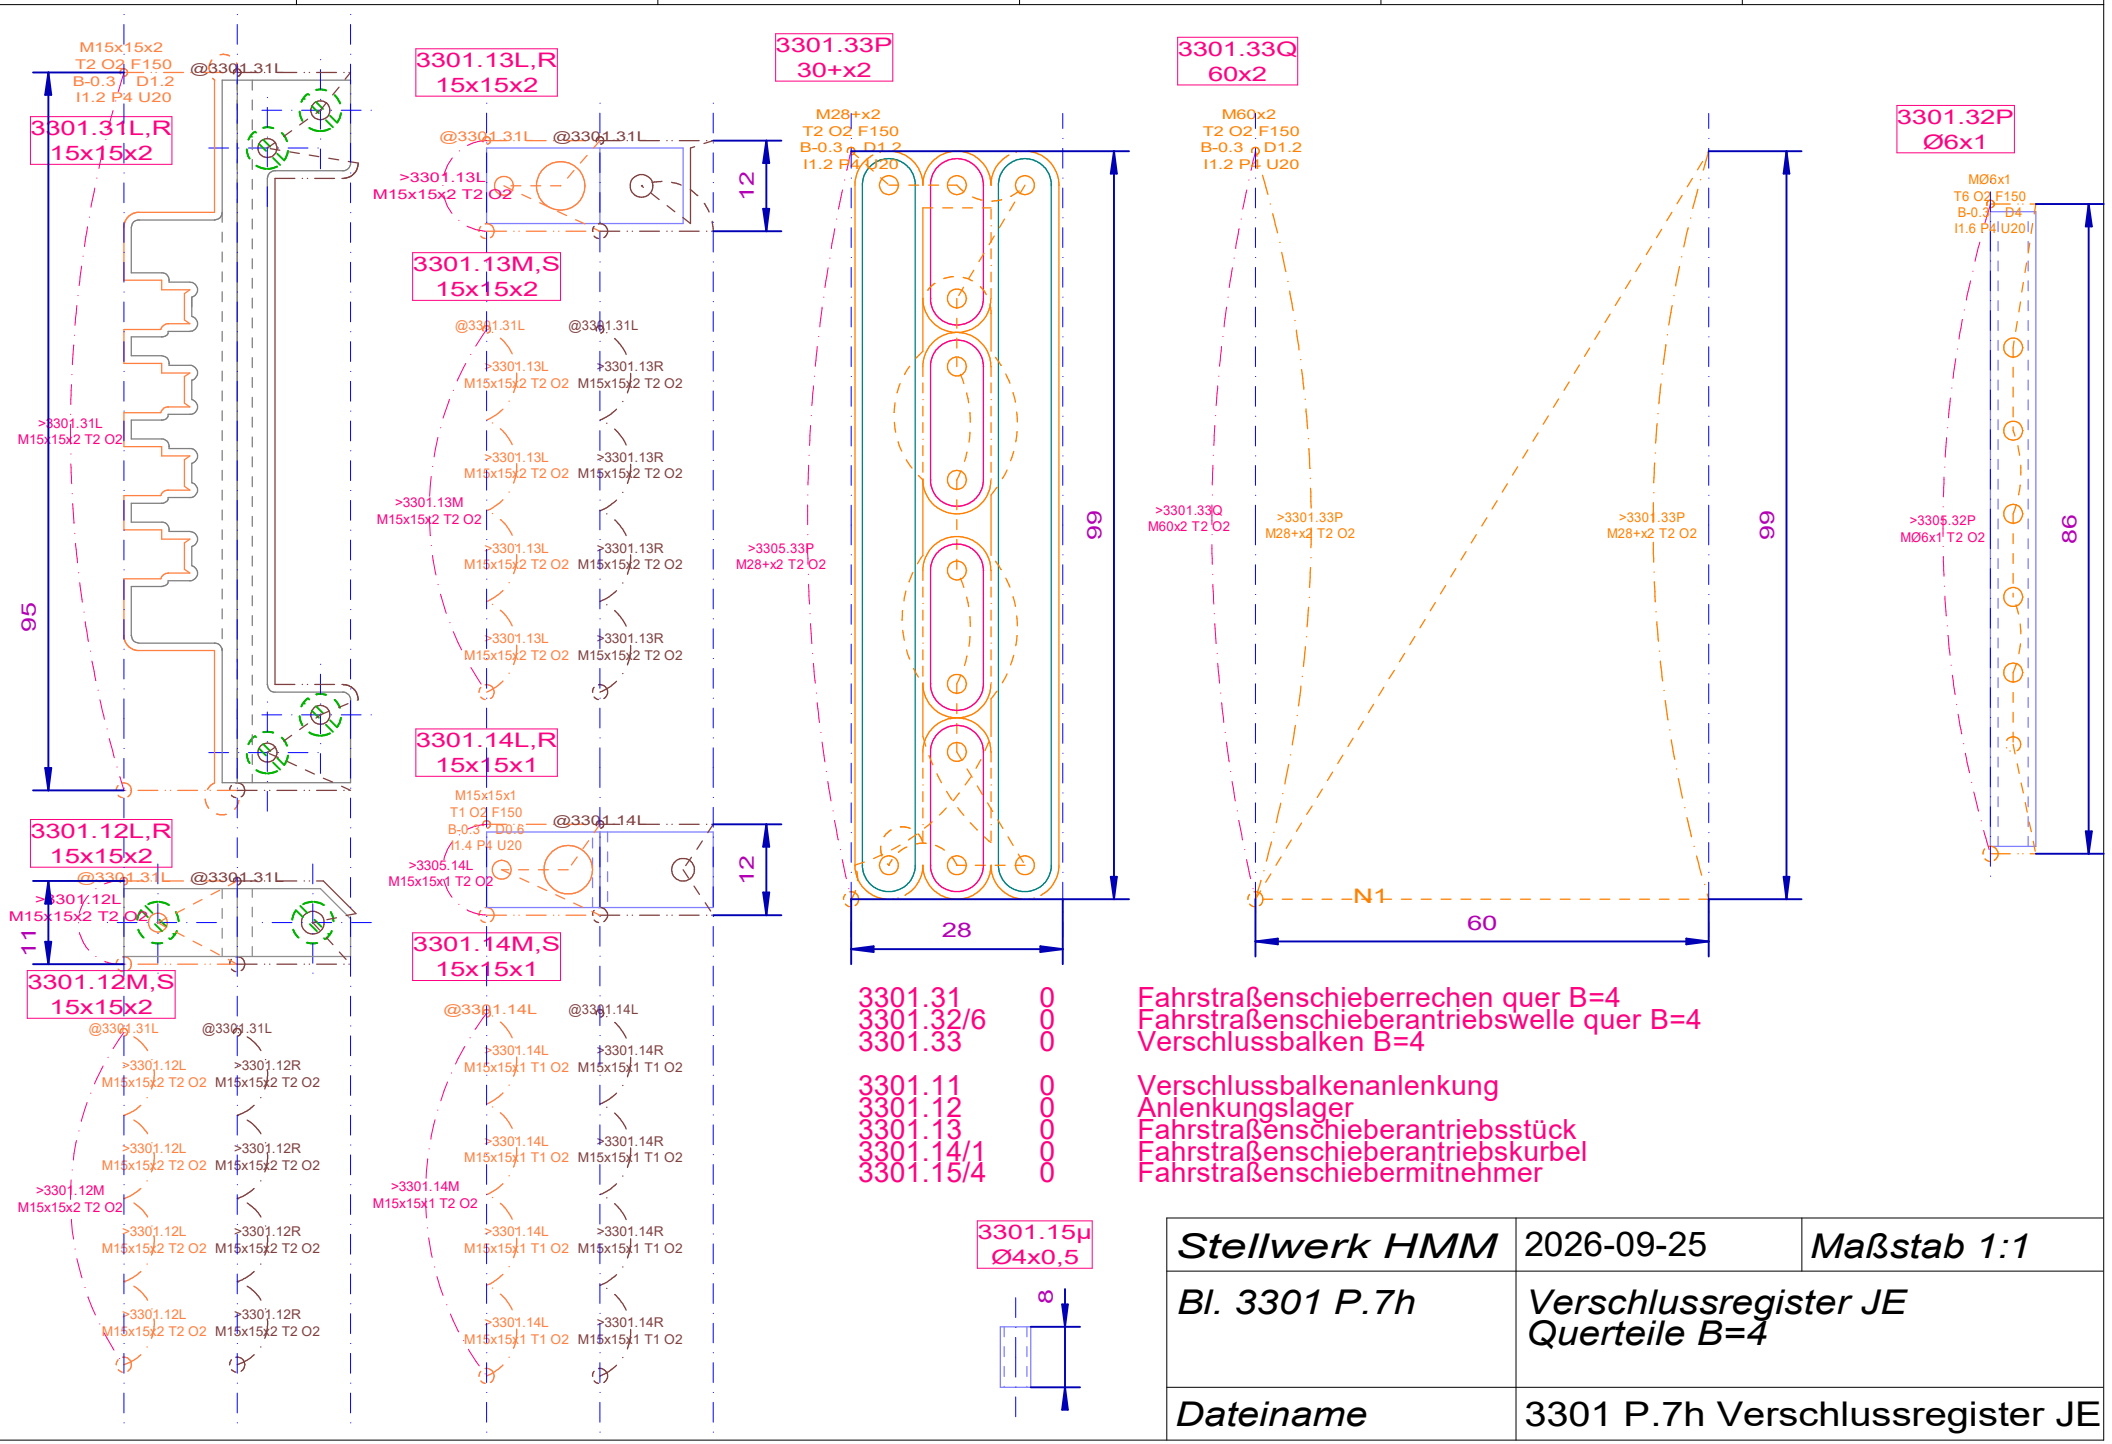

1
2
3
4
5
6
A
B
C
D
3301.31L,R
15x15x2
M15x15x2
T2 O2 F150
B-0.3 D1.2
I1.2 P4 U20
@3301.31L
>3301.31L
M15x15x2 T2 O2
95
3301.12L,R
15x15x2
>3301.12L
M15x15x2 T2 O2
11
3301.12M,S
15x15x2
>3301.12M
M15x15x2 T2 O2
3301.13L,R
15x15x2
>3301.13L
M15x15x2 T2 O2
12
3301.13M,S
15x15x2
>3301.13M
M15x15x2 T2 O2
>3301.13R
M15x15x2 T2 O2
3301.14L,R
15x15x1
M15x15x1
T1 O2 F150
B-0.3 D0.6
I1.4 P4 U20
@3301.14L
>3305.14L
M15x15x1 T2 O2
12
3301.14M,S
15x15x1
>3301.14M
M15x15x1 T2 O2
>3301.14R
M15x15x1 T1 O2
3301.33P
30+x2
M28+x2
T2 O2 F150
B-0.3 D1.2
I1.2 P4 U20
>3305.33P
M28+x2 T2 O2
99
28
3301.33Q
60x2
M60x2
T2 O2 F150
B-0.3 D1.2
I1.2 P4 U20
>3301.33Q
M60x2 T2 O2
>3301.33P
M28+x2 T2 O2
N1
60
3301.32P
Ø6x1
MØ6x1
T6 O2 F150
B-0.3 D4
I1.6 P4 U20
>3305.32P
MØ6x1 T2 O2
86
3301.15µ
Ø4x0,5
8
3301.31 0 Fahrstraßenschieberrechen quer B=4
3301.32/6 0 Fahrstraßenschieberantriebswelle quer B=4
3301.33 0 Verschlussbalken B=4
3301.11 0 Verschlussbalkenanlenkung
3301.12 0 Anlenkungslager
3301.13 0 Fahrstraßenschieberantriebsstück
3301.14/1 0 Fahrstraßenschieberantriebskurbel
3301.15/4 0 Fahrstraßenschiebermitnehmer
Stellwerk HMM
2026-09-25
Maßstab 1:1
Bl. 3301 P.7h
Verschlussregister JE
Querteile B=4
Dateiname
3301 P.7h Verschlussregister JE