


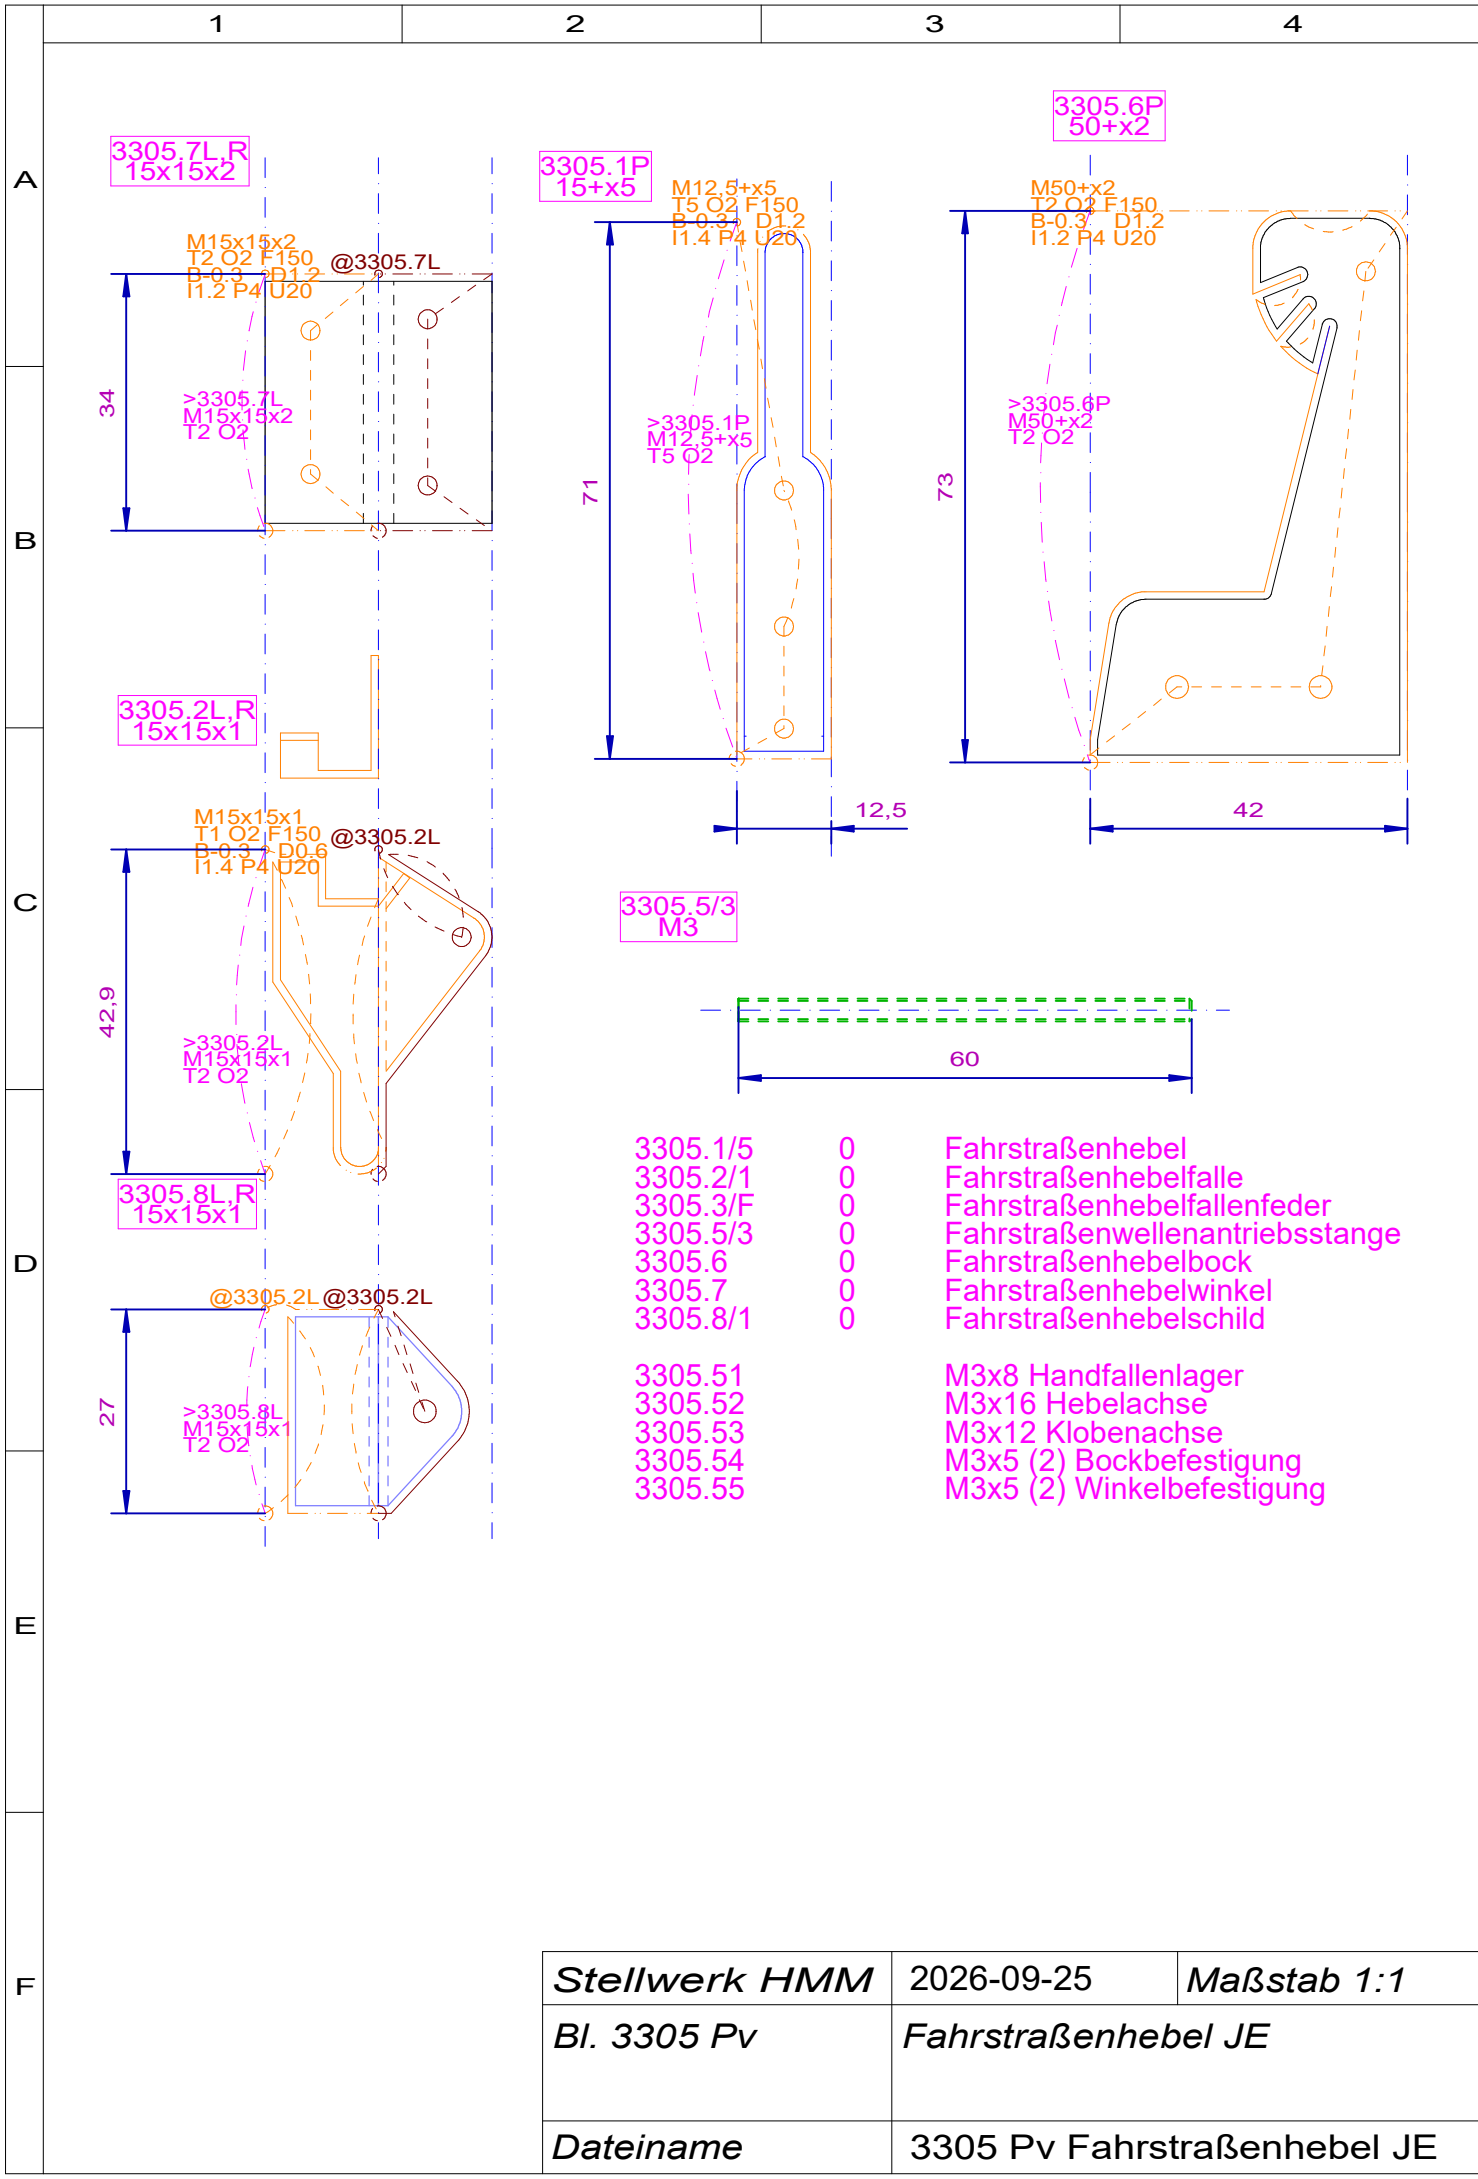

- |          |   |                                 |
|----------|---|---------------------------------|
| 3305.1/5 | 0 | Fahrstraßenhebel                |
| 3305.2/1 | 0 | Fahrstraßenhebelfalle           |
| 3305.3/F | 0 | Fahrstraßenhebelfallenfeder     |
| 3305.5/3 | 0 | Fahrstraßenwellenantriebsstange |
| 3305.6   | 0 | Fahrstraßenhebelbock            |
| 3305.7   | 0 | Fahrstraßenhebelwinkel          |
| 3305.8/1 | 0 | Fahrstraßenhebelschild          |
|          |   |                                 |
| 3305.51  |   | M3x8 Handfallenlager            |
| 3305.52  |   | M3x16 Hebelachse                |
| 3305.53  |   | M3x12 Klobenachse               |
| 3305.54  |   | M3x5 (2) Bockbefestigung        |
| 3305.55  |   | M3x5 (2) Winkelbefestigung      |

|               |                             |             |
|---------------|-----------------------------|-------------|
| Stellwerk HMM | 2026-09-25                  | Maßstab 1:1 |
| Bl. 3305 Pv   | Fahrstraßenhebel JE         |             |
| Dateiname     | 3305 Pv Fahrstraßenhebel JE |             |