



Verschlussanordnung

A

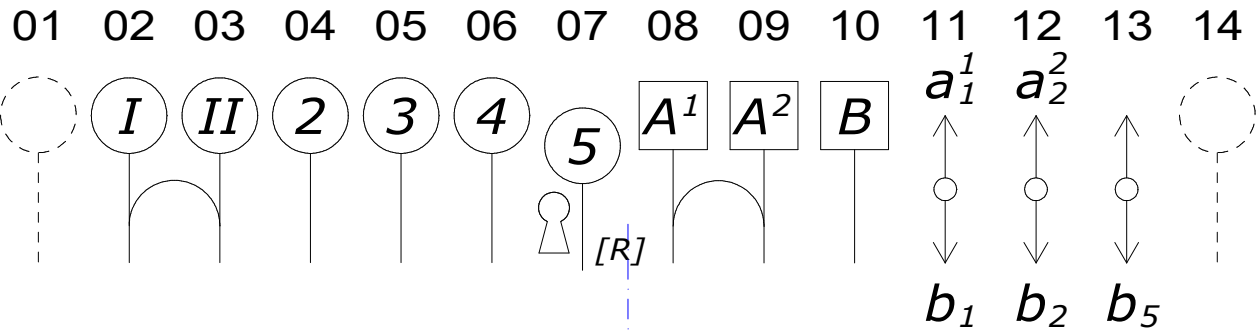

B

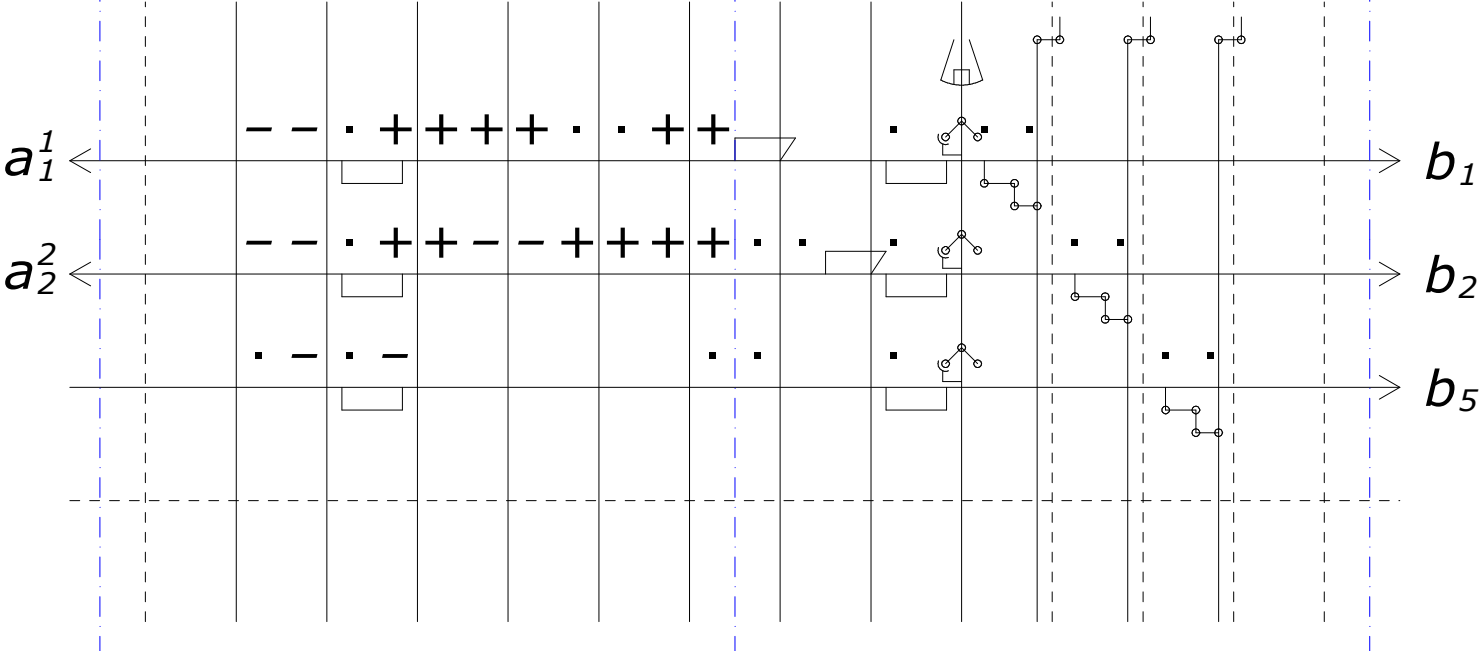

C

D

Anmerkungen:
a) Die Verschlussanordnung ist aus der Sicht von vorne dargestellt (im Gegensatz zur Darstellung für Einheitsstellwerke);
b) Die Symbole für Signalverschlussstücke und Gruppenverschlüsse habe ich erfunden, weil ich keine Unterlagen mit Symbolen dafür kenne.

Stellwerk HMM	2026-09-23	ohne Maßstab
Bl. 3813 Lh	Tegernsee Verschlussanordnung	
Dateiname	3813 Lh Verschlussanordnung Tegernsee	