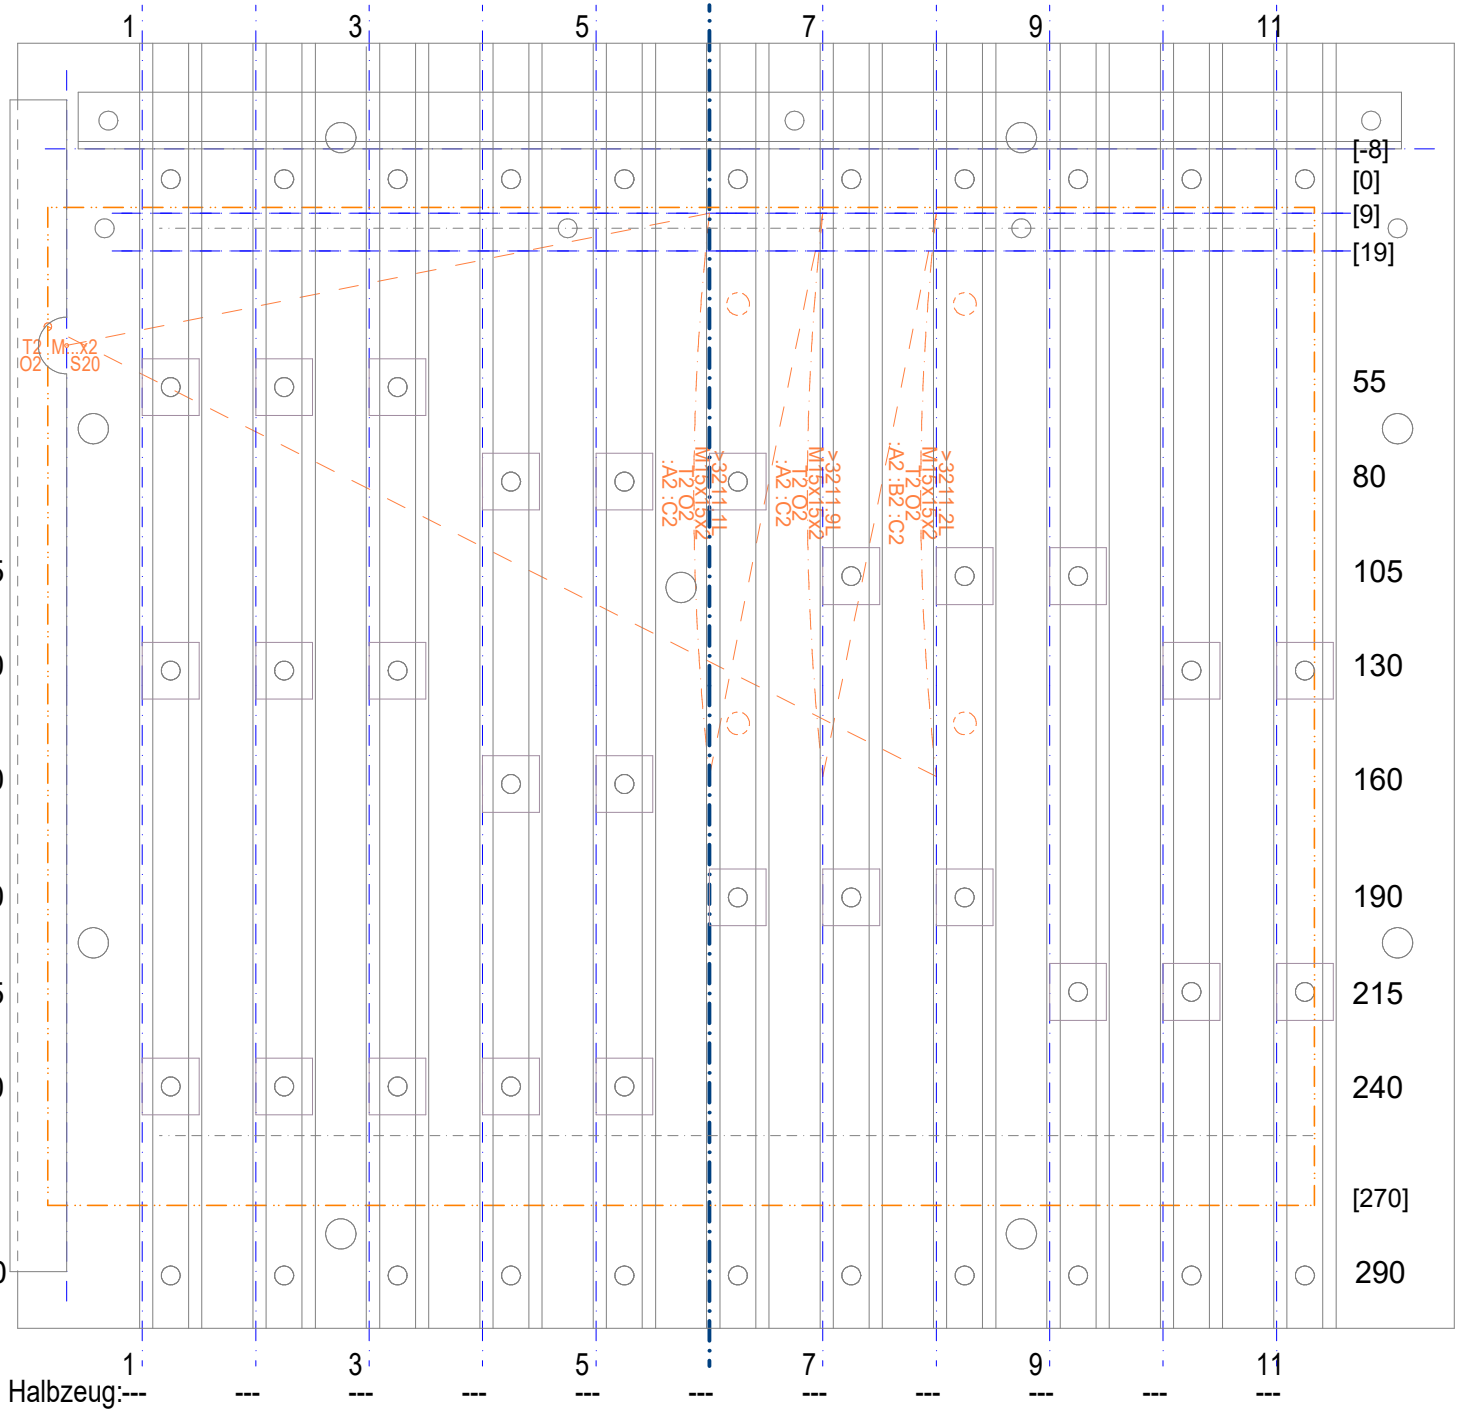

Stückliste 1084:

15x15x2
2x 2052.1

15x15x1
2x 2052.4

25x2 oder 50x2
2x 2053.2

Stellwerk HMM	*Maßstab 1:2*
2026-05-08	*Bl. 3808 S.9aLh*
Hebelbank 2 Aufspannpfad	
Dateiname	3808 S.9aLh Hebelbank 2