


A

B

C

D

Tegernsee

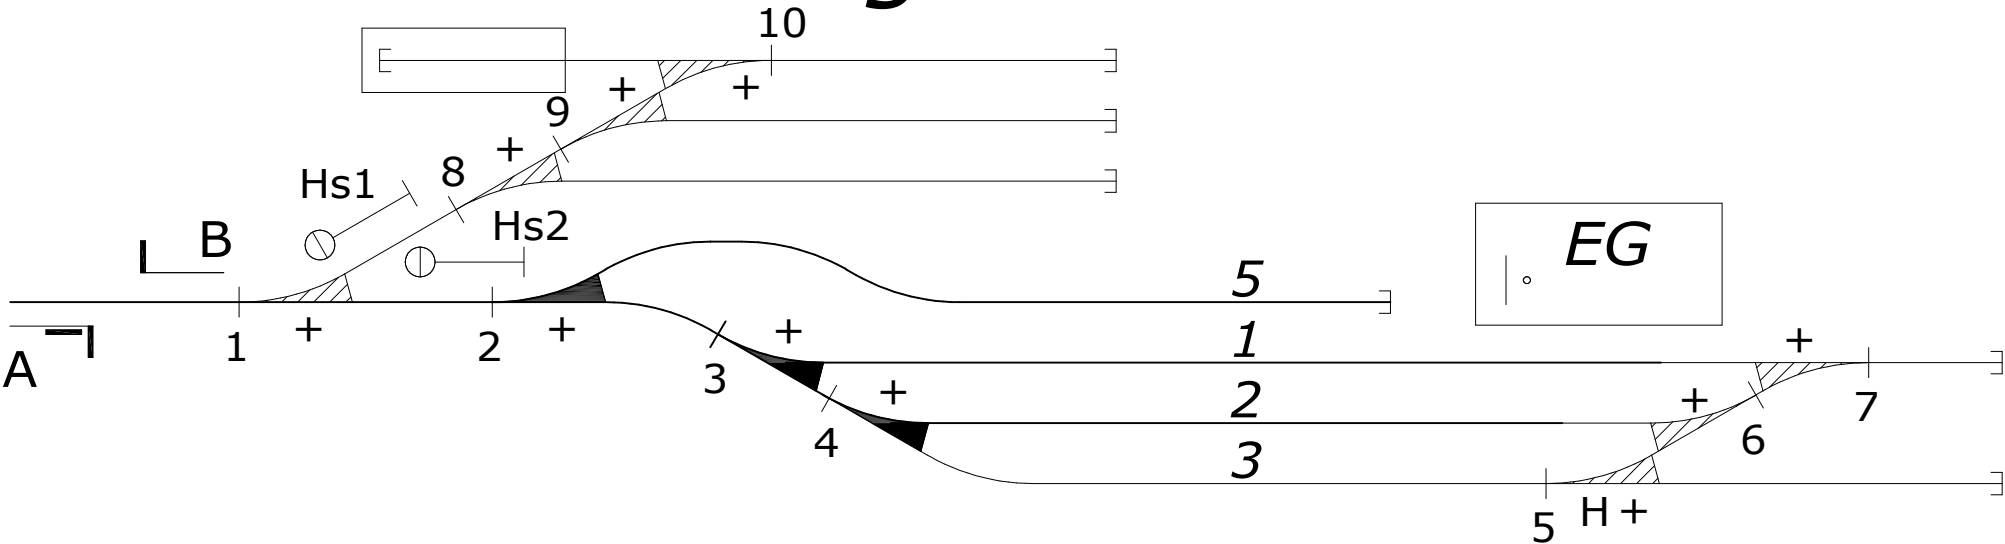

	11		12		13	08	09	10	01	02	03	04	05	06
	a_1^1	a_2^2	b_1	b_2	b_5	A^1	A^2	B	I	II	2	3	4	5
a_1^1	-	+	+	+	+	↙			-		+	+		+
a_2^2	+	-	+	+	+		↘		-		+	-	+	+
b_1	+	+	-	+	+			↙		-	+	+		+
b_2	+	+	+	-	+			↙		-	+	-	+	+
b_5	+	+	+	+	-			↙		-	-			

Gr.st.: Hs1 ⊙, Hs2 ⊙,
I-: Hs1 ⊙, Hs2 ⊙, 1+
II-: Hs1 ⊙, Hs2 ⊙, 1+

Schlüssel- formen	I*	II*	2	3	4	5
						+:R

Stellwerk HMM	2026-06-14	ohne Maßstab
Bl. 3811 Lh	Tegernsee Lage- und Verschlussplan	
Dateiname	3811 Lh Lage- und Verschlussplan Tegernsee	