


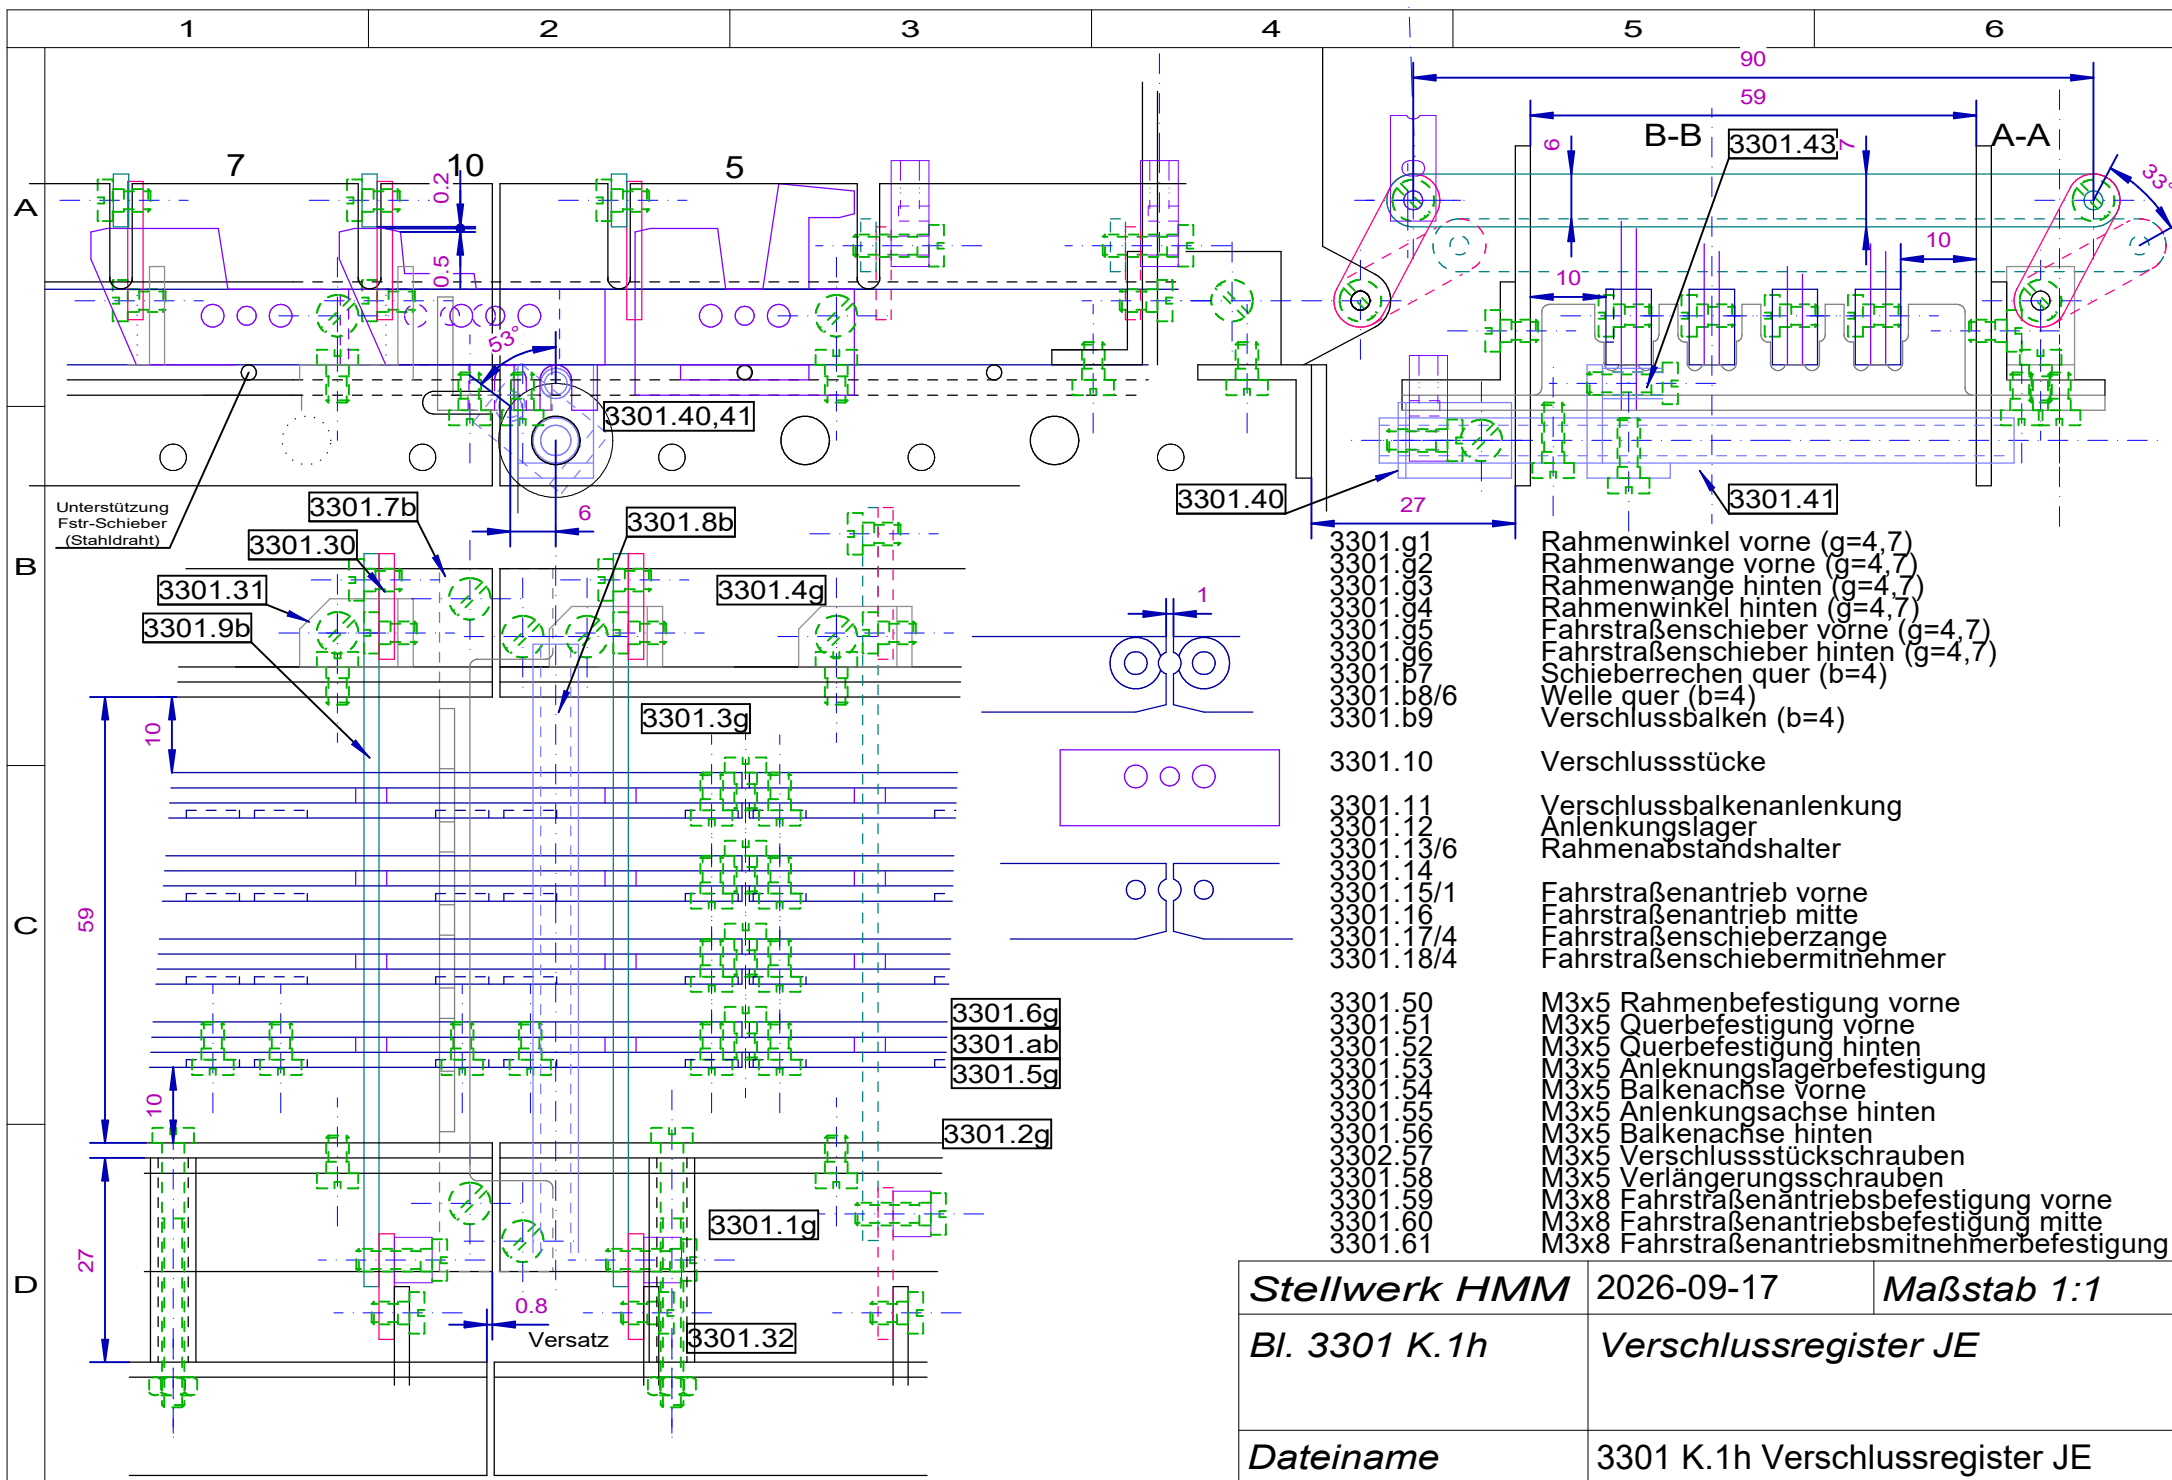

Stellwerk HMM	2026-09-17	Maßstab 1:1
Bl. 3301 K.1h	Verschlussregister JE	
Dateiname	3301 K.1h Verschlussregister JE	