


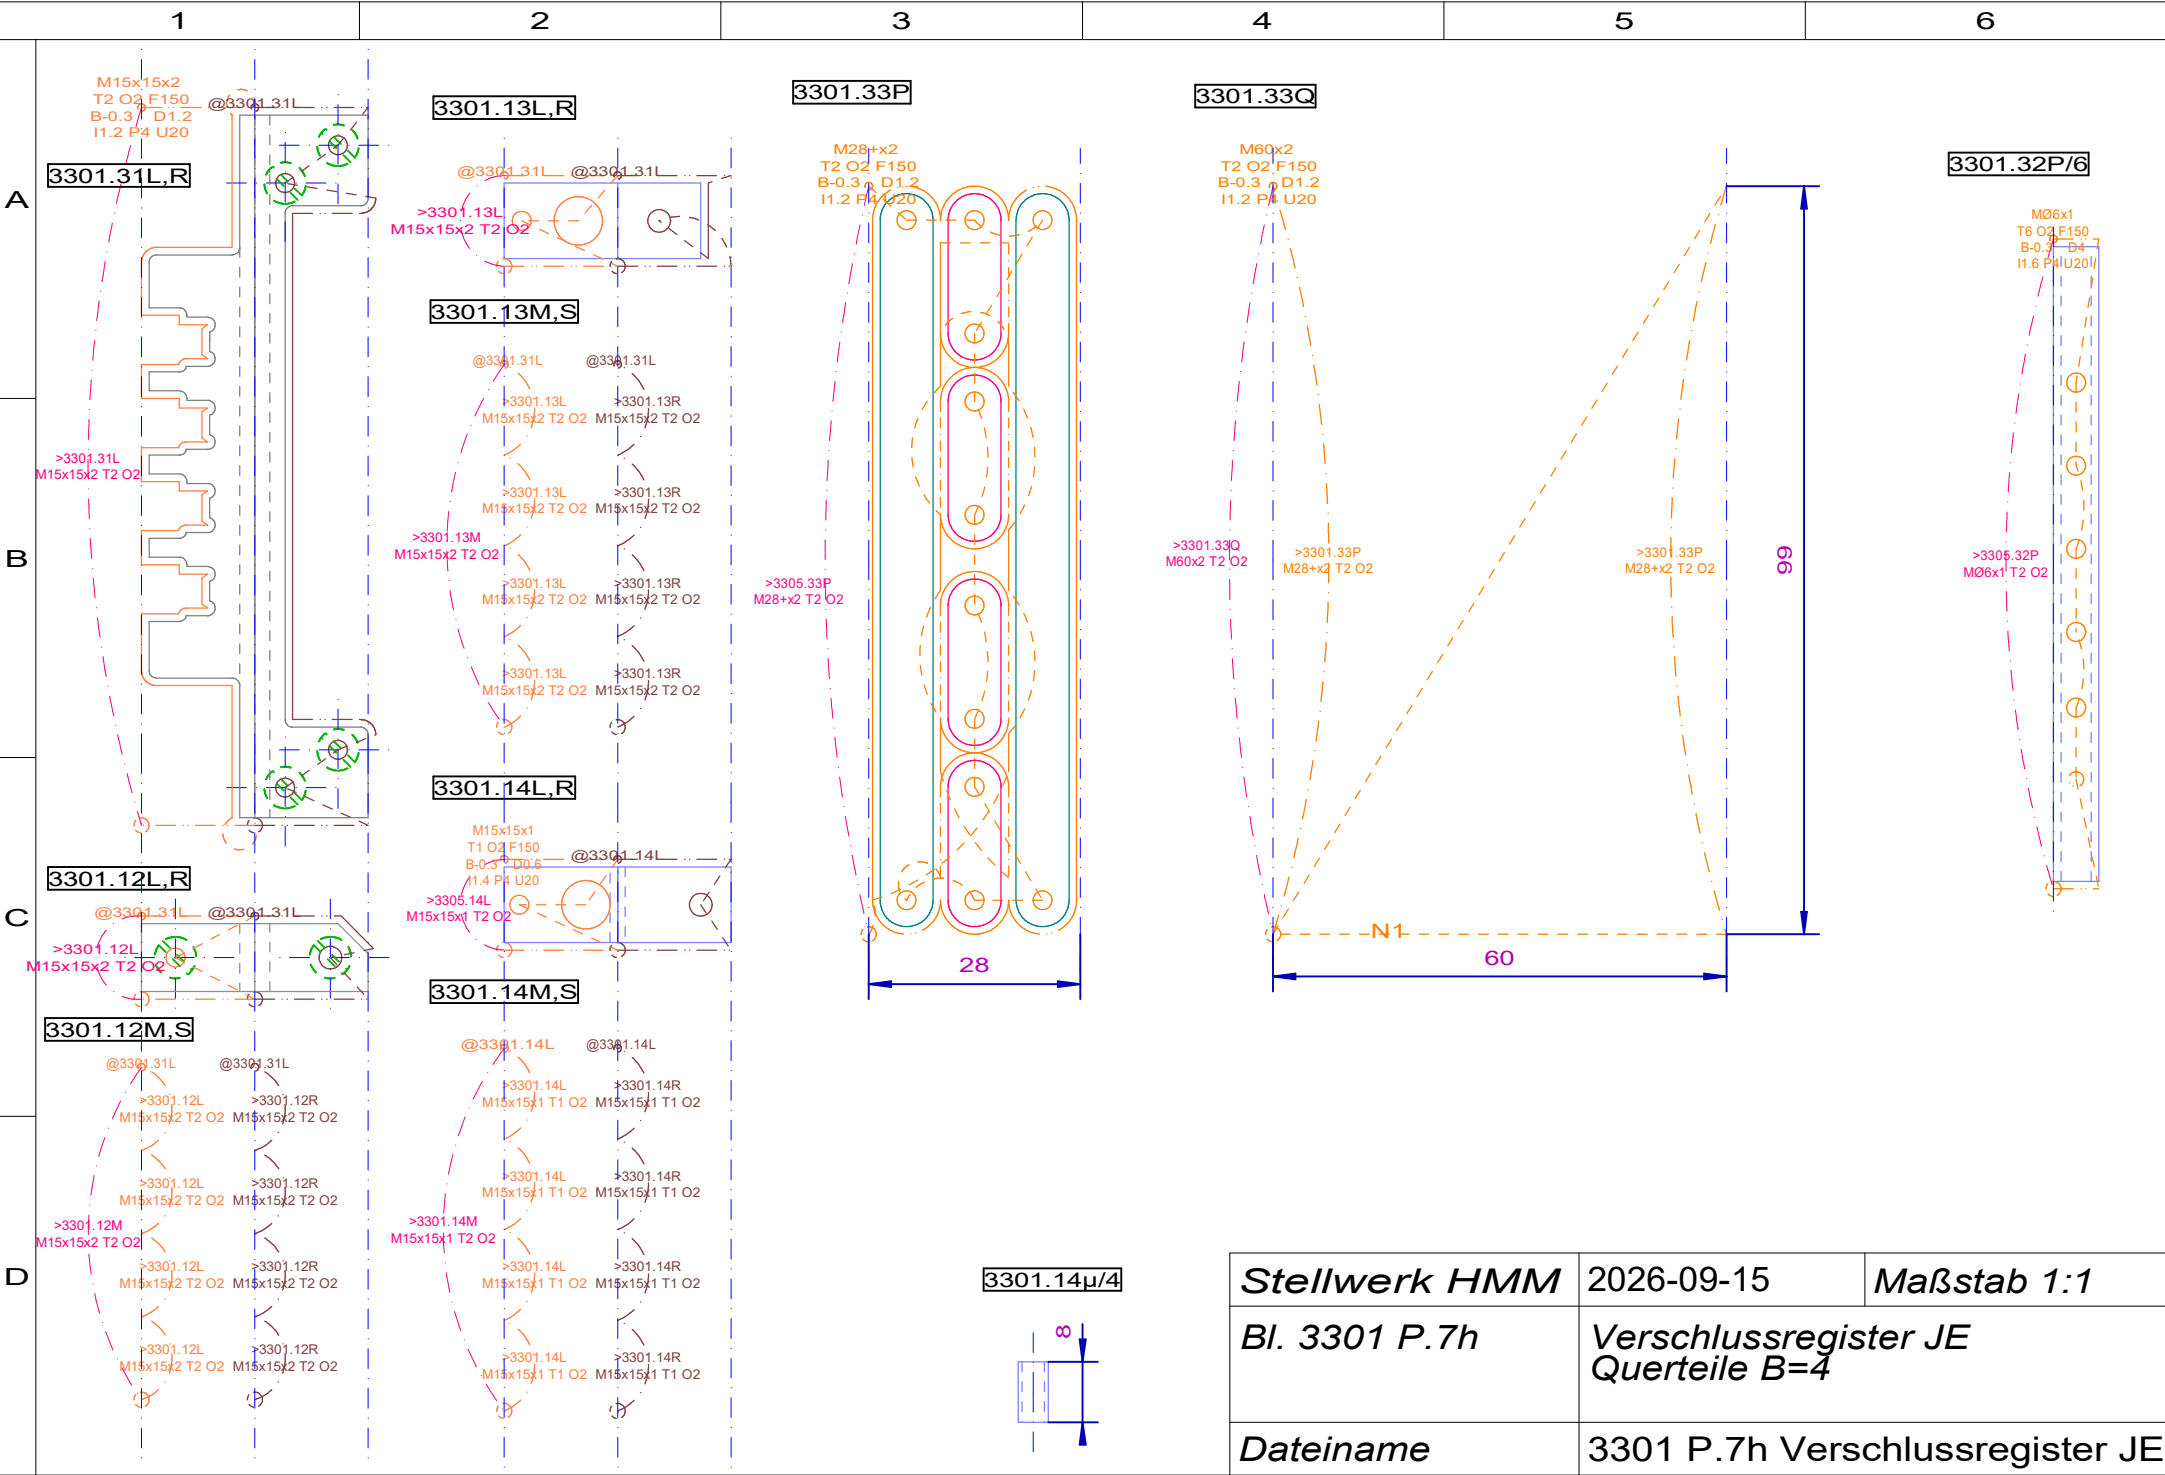

Stellwerk HMM	2026-09-15	Maßstab 1:1
Bl. 3301 P.7h	Verschlussregister JE Querteile B=4	
Dateiname	3301 P.7h Verschlussregister JE	