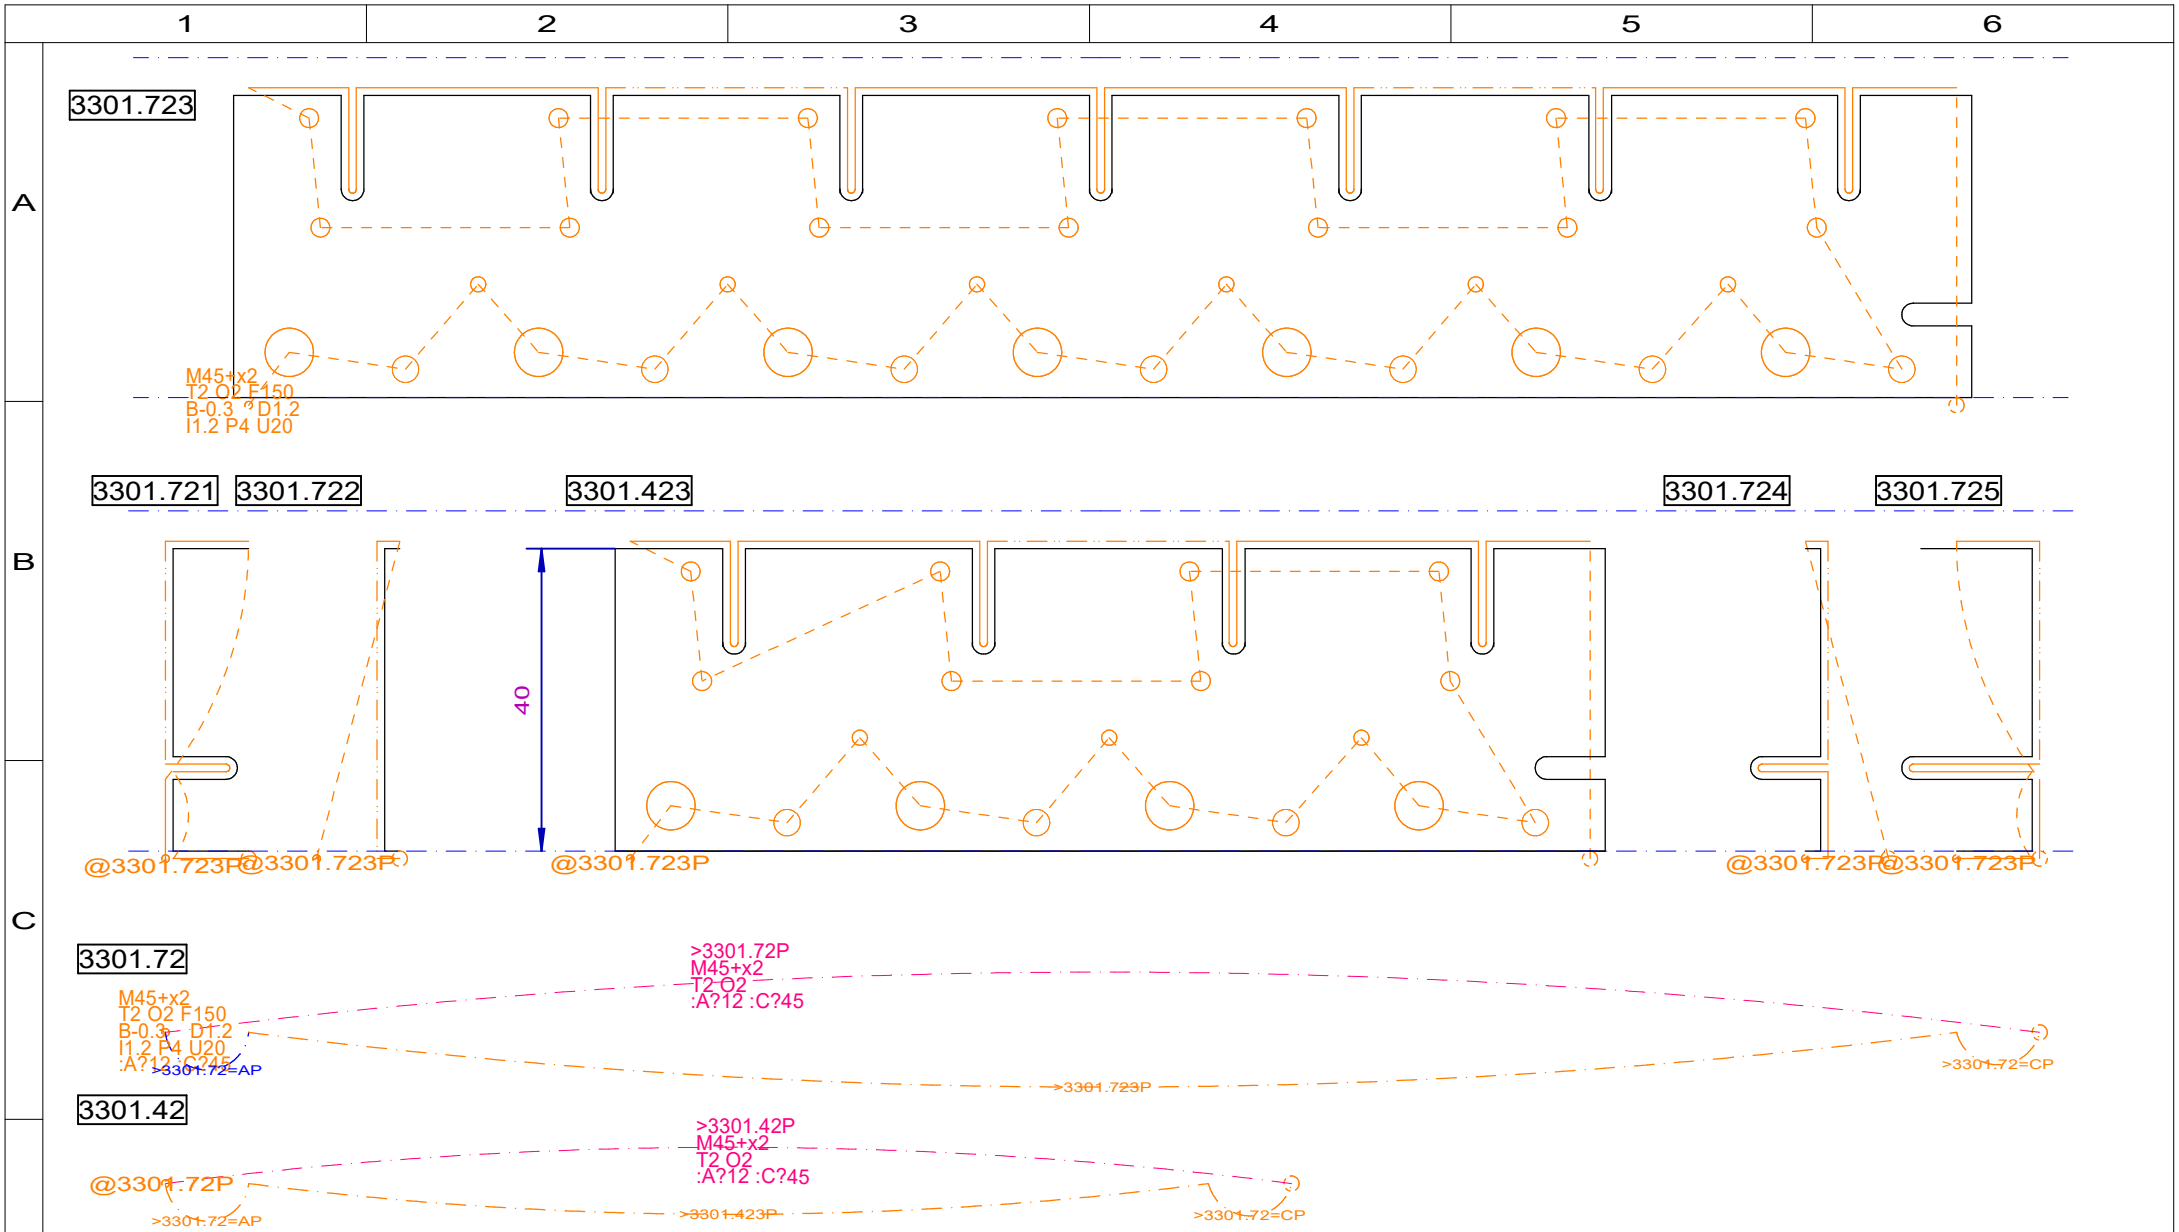


3301.42	0	Rahmenwange vorne L=4 :A1 linkes Ende lang, :A2 linkes Ende kurz :C4 rechtes Ende kurz, :C5 rechtes Ende lang
3301.72	0	Rahmenwange vorne L=7 :A1 linkes Ende lang, :A2 linkes Ende kurz :C4 rechtes Ende kurz, :C5 rechtes Ende lang

Stellwerk HMM	2026-09-12	*Maßstab 1:1*
Bl. 3301 P.2h	*Verschlussregister JE* *Rahmen vorne L=4 und L=7*	
Dateiname	3301 P.2h Verschlussregister JE	