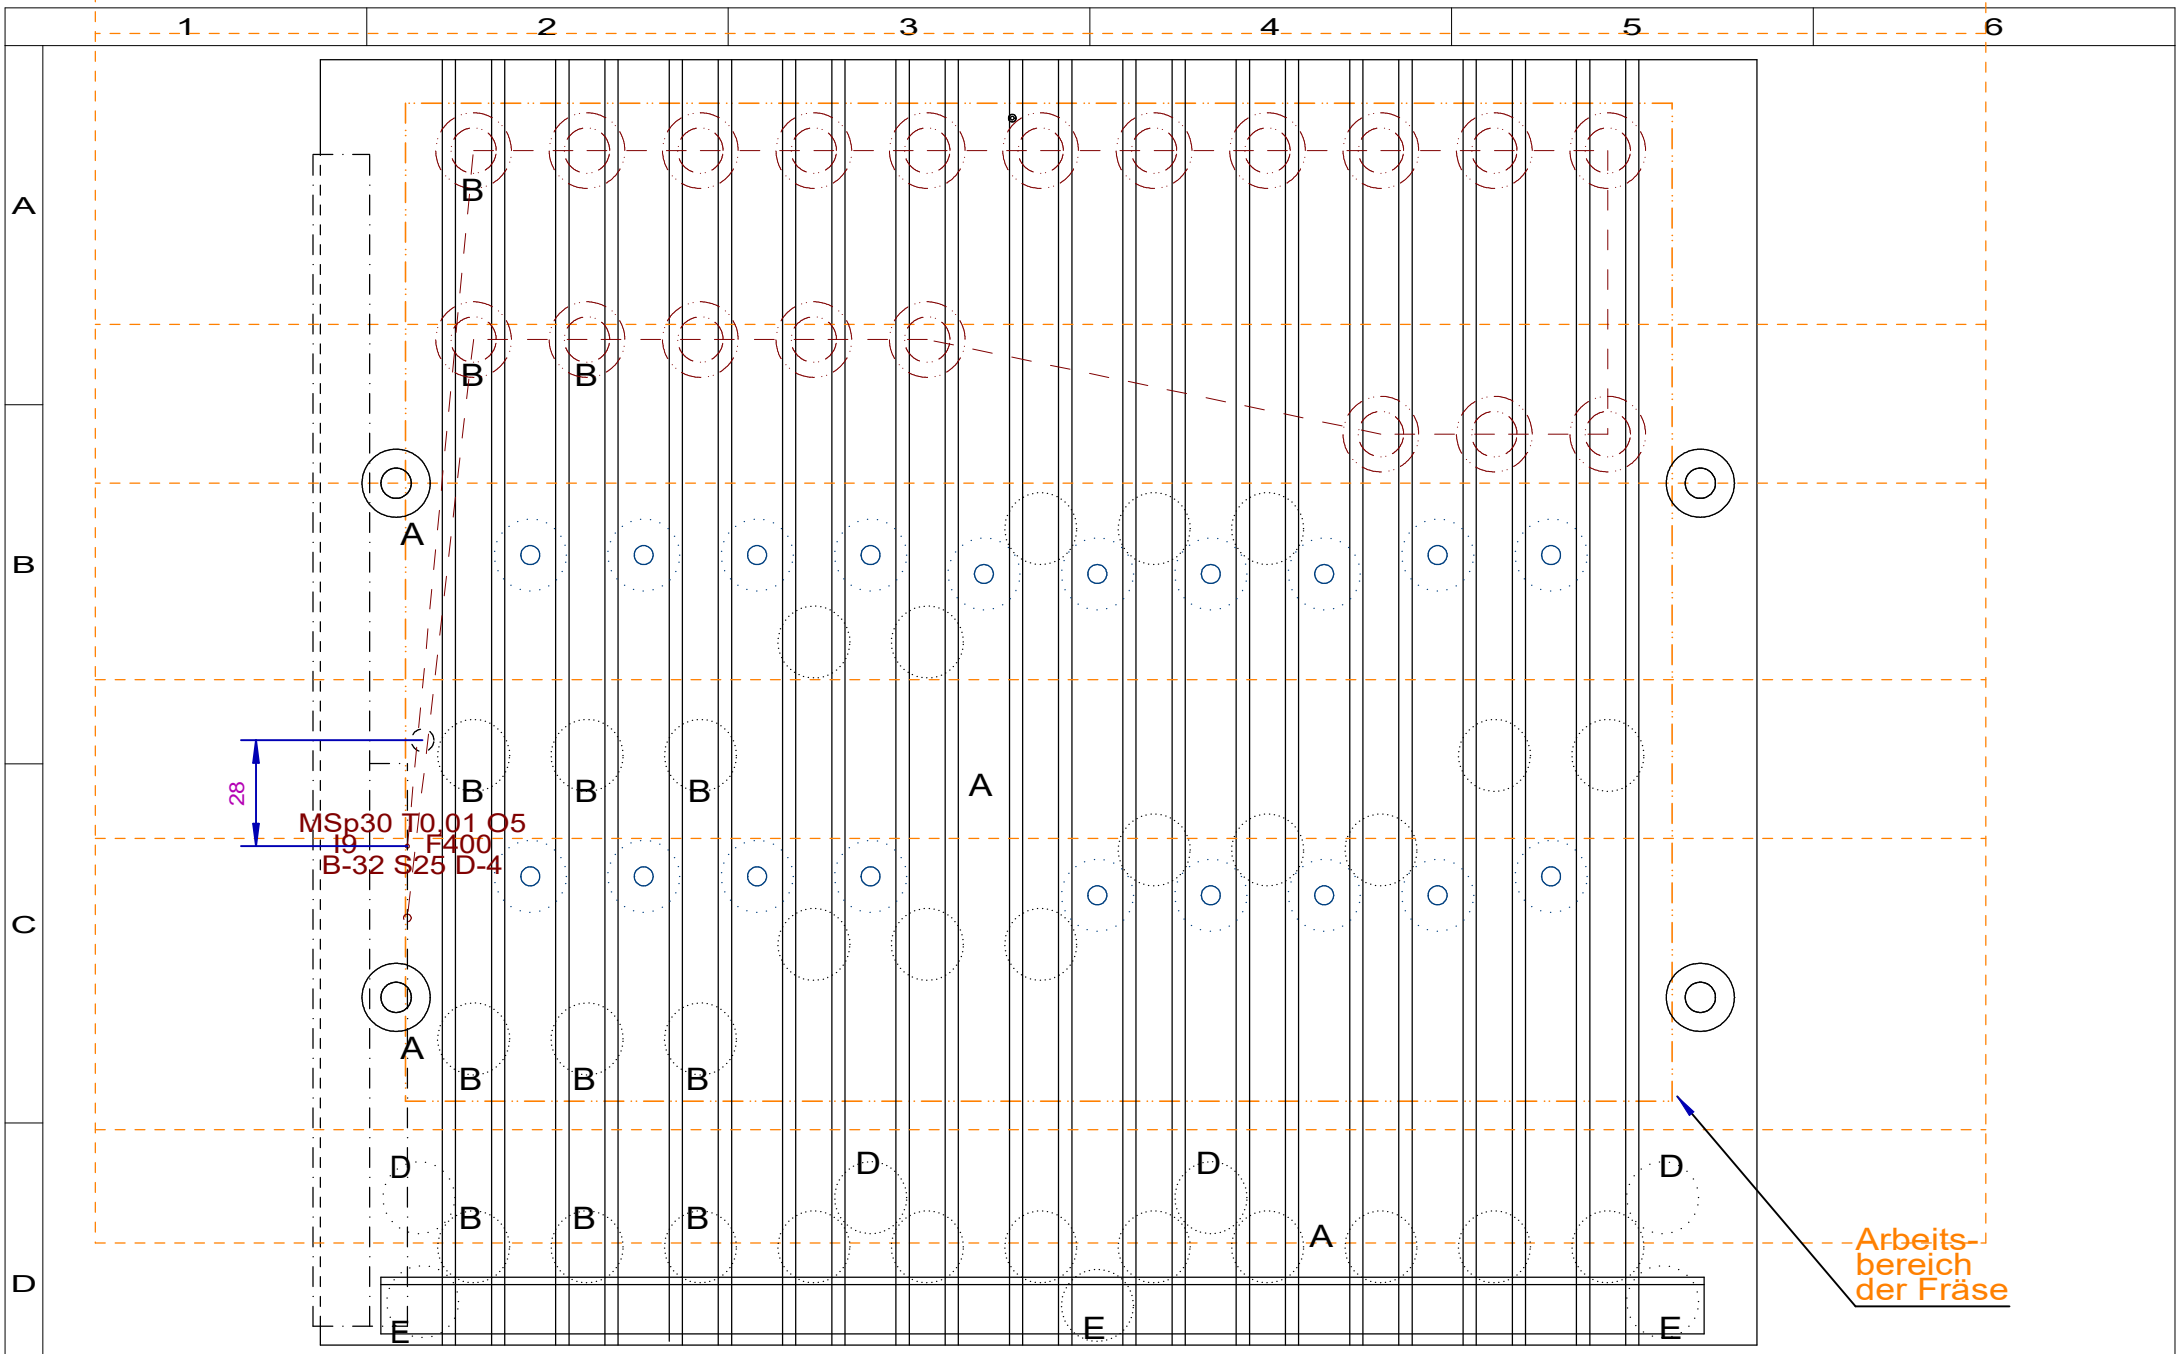


A M8 Opferplatte auf Schlitten
B M5 Werkstücke/Halbzeuge
D M5 Wiederholungsleiste
E M5 Oberer Anschlag
F M5 Festhaltungen

Stellwerk HMM	2026-09-10	*1:2*	*Dateiname*
Bl. 2913 P.4Vh	*Fräse - Aufspannplatte*		2913 P.4Vh Aufspannplatte unten vo