


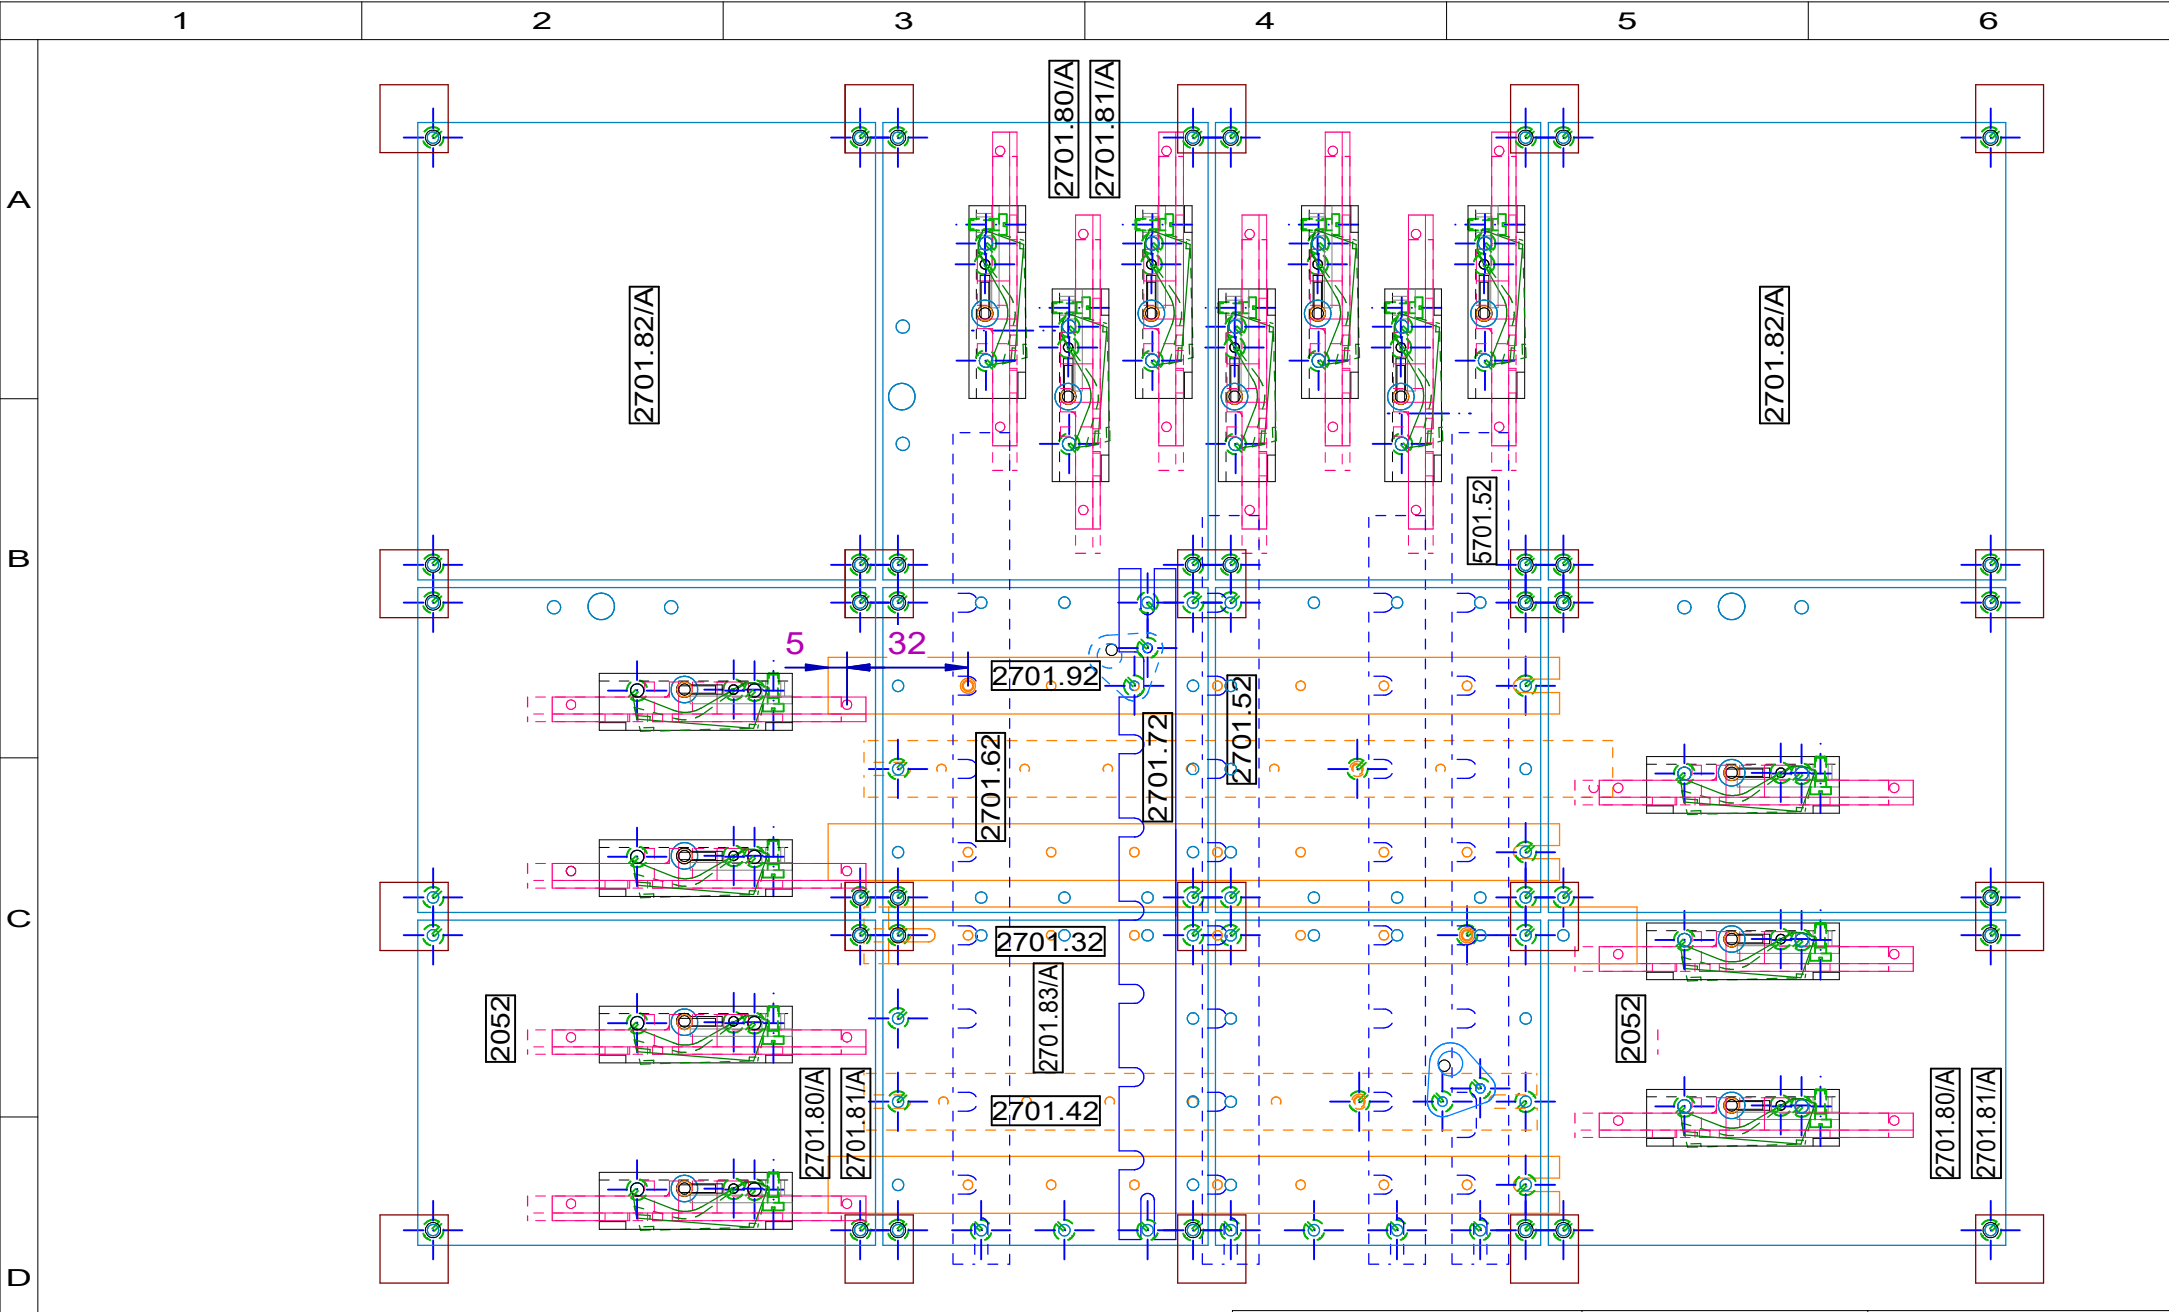

Stellwerk HMM	2026-07-19	Maßstab 1:2
Bl. 2701 K.3h	Schlüsselwerk vertikal	
Dateiname	2701 K.3h Schlüsselwerk	