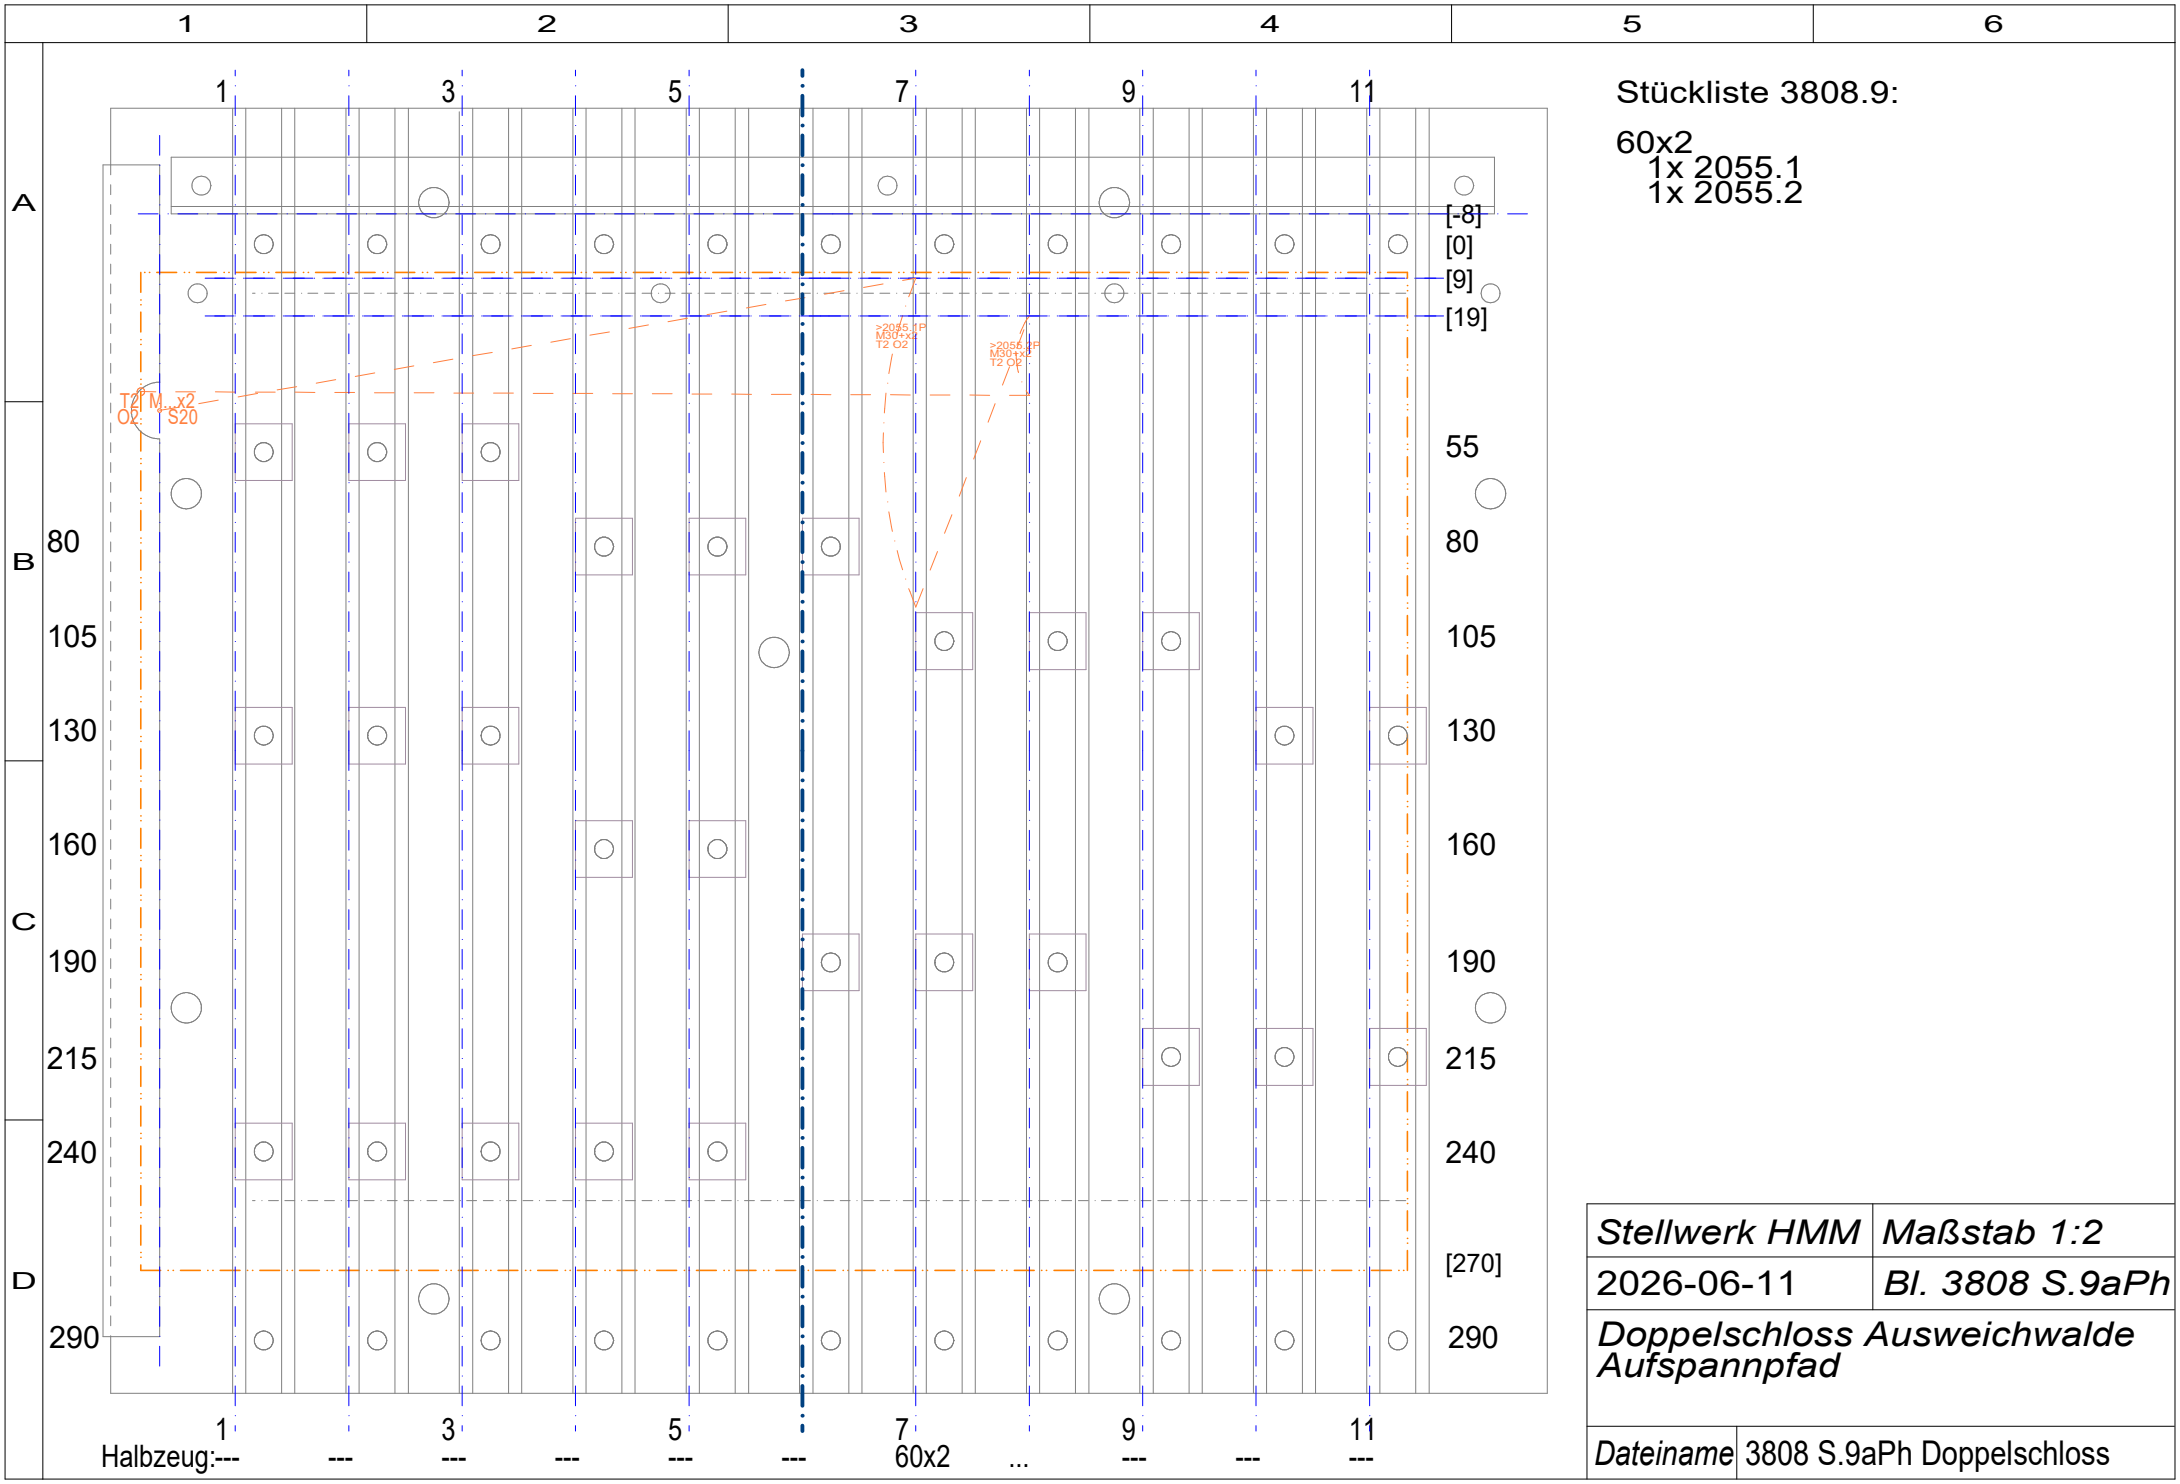

Stückliste 3808.9:

60x2
1x 2055.1
1x 2055.2

Stellwerk HMM	*Maßstab 1:2*
2026-06-11	*Bl. 3808 S.9aPh*
Doppelschloss Ausweichwalde Aufspannpfad	
Dateiname	3808 S.9aPh Doppelschloss